
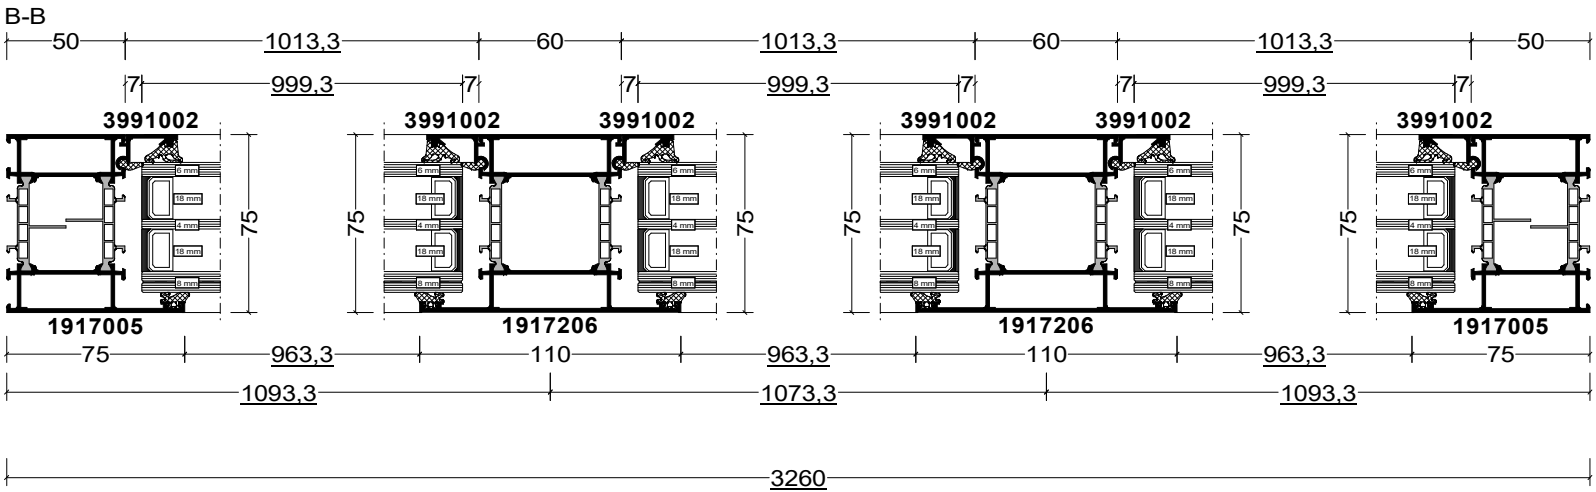
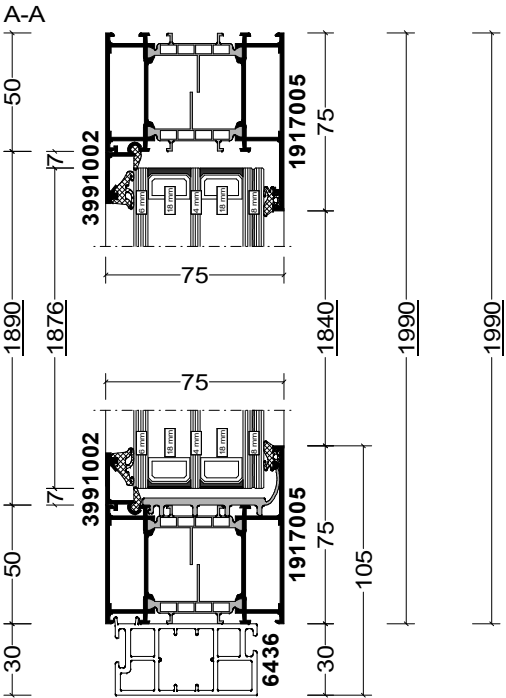


Pos. 001, Anzahl: 1
Oberfläche: RAL 9016, matt
Kommission: Bergwerk Frieden Schwendt
Auftragsnummer: TFU254696BR
Außenansicht

Element unverglast, Gläser lose
30mm Basisprofil montiert

3x U401 . Isolierglas 0,5, Superspacer schwarz
54mm 1,87 m² 999 x 1876mm
außen: 207 | VSG 8 0.76 wärm.
mitte: 4mm
innen: 106 | ESG 6 wärmebesch

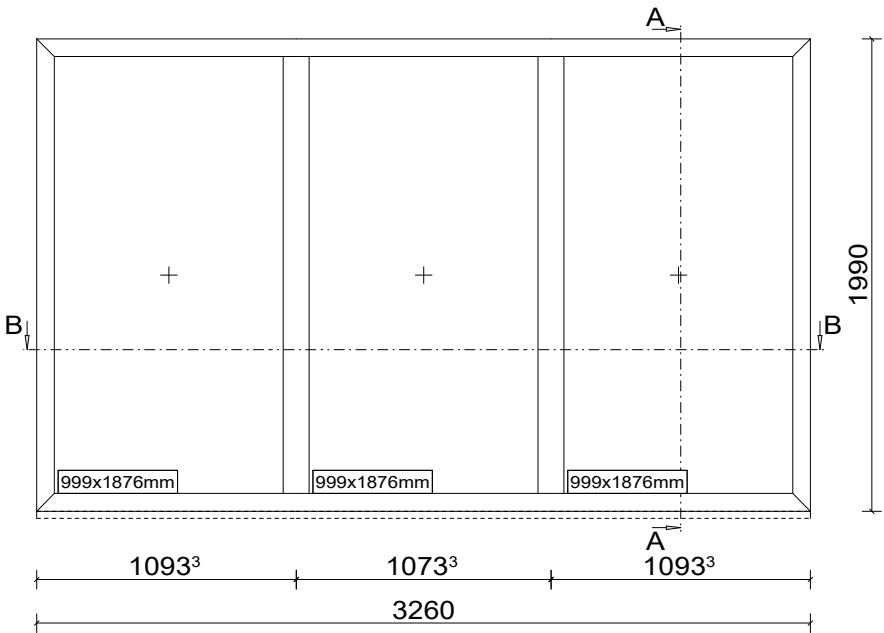

System: WL/WS 75 EVO	Datum: 21.10.2025	
	Z-Nr.: 001	
BVH: Bergwerk Frieden Schwendt	Auftrag: TFU254696BR	