


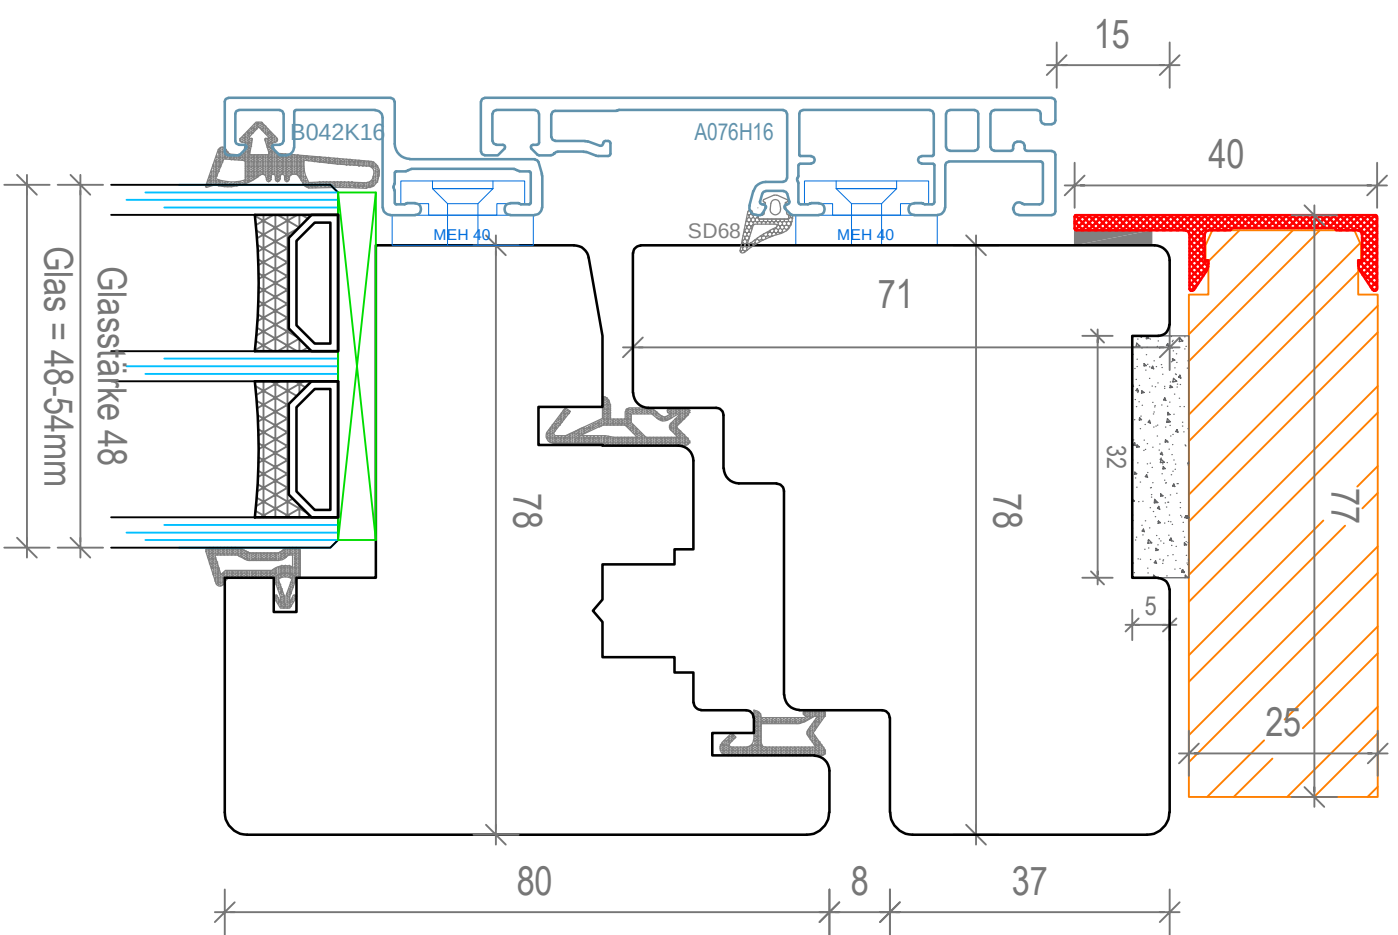



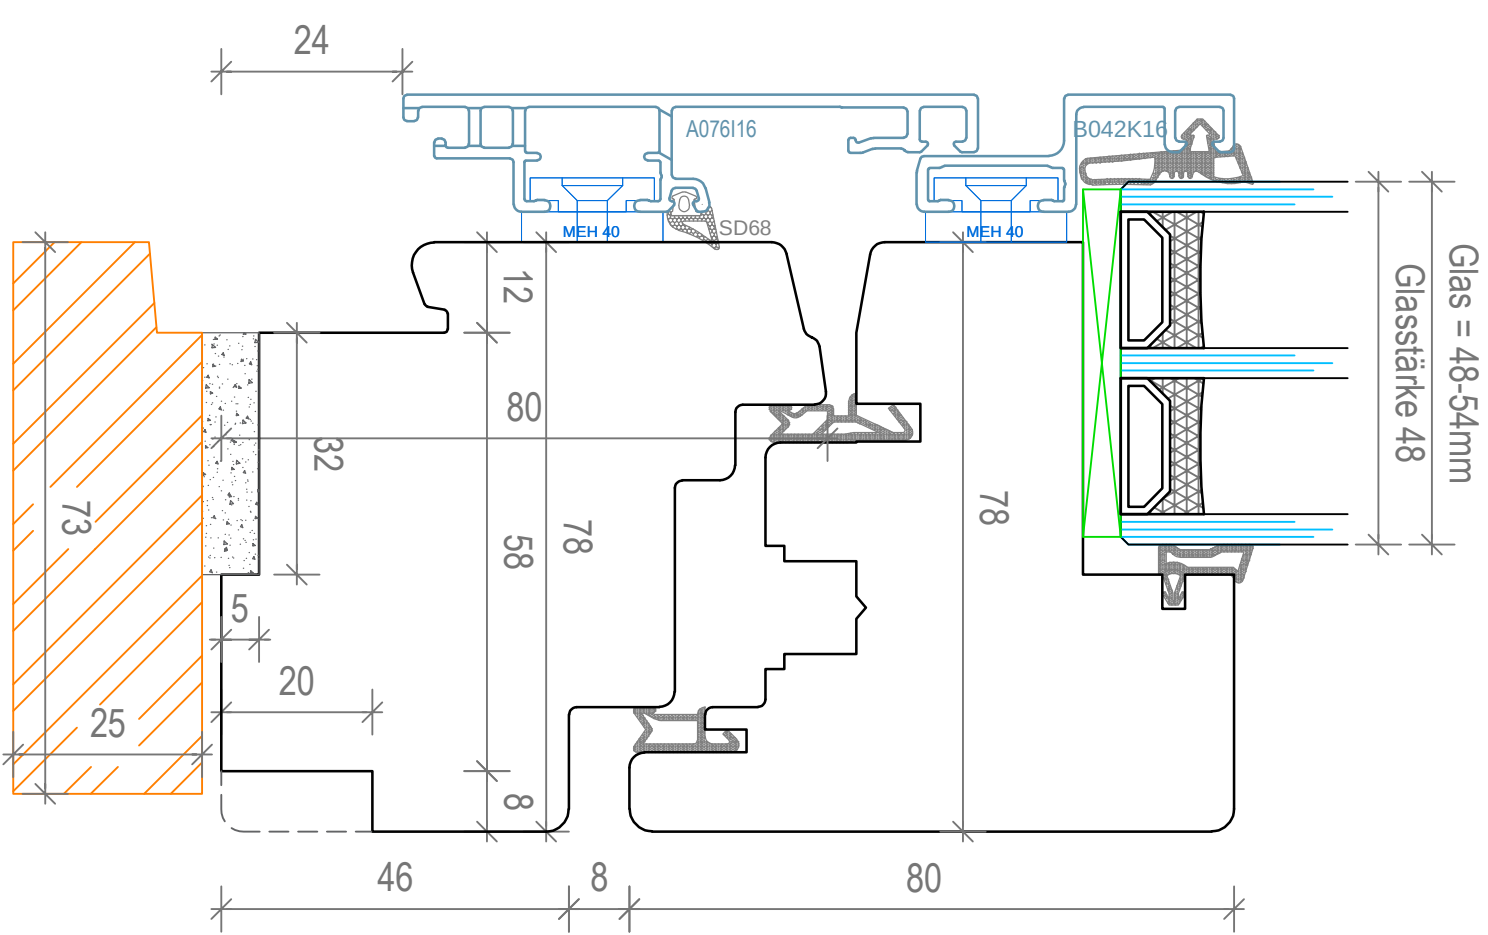



|   |                                                                    |                              |                                                   |
|---|--------------------------------------------------------------------|------------------------------|---------------------------------------------------|
|  <b>Rieder</b><br><b>ZILLERTAL</b> | <b>Rieder GmbH &amp; Co KG</b>                                     |                              | <b>Maßstab:</b><br>1:1                            |
|   | Landstraße 33<br>6273 Ried im Zillertal<br>www.rieder-zillertal.at |                              |                                                   |
| Detail oben und seitlich mit Blindstock                                                                             |                                                                    | <b>Holz/Alu</b><br><b>98</b> | <b>Technisch:</b><br>SPD<br>Jänner 2024<br>Stand: |
| Fenster und Balkontür                                                                                               |                                                                    | gerade                       |                                                   |

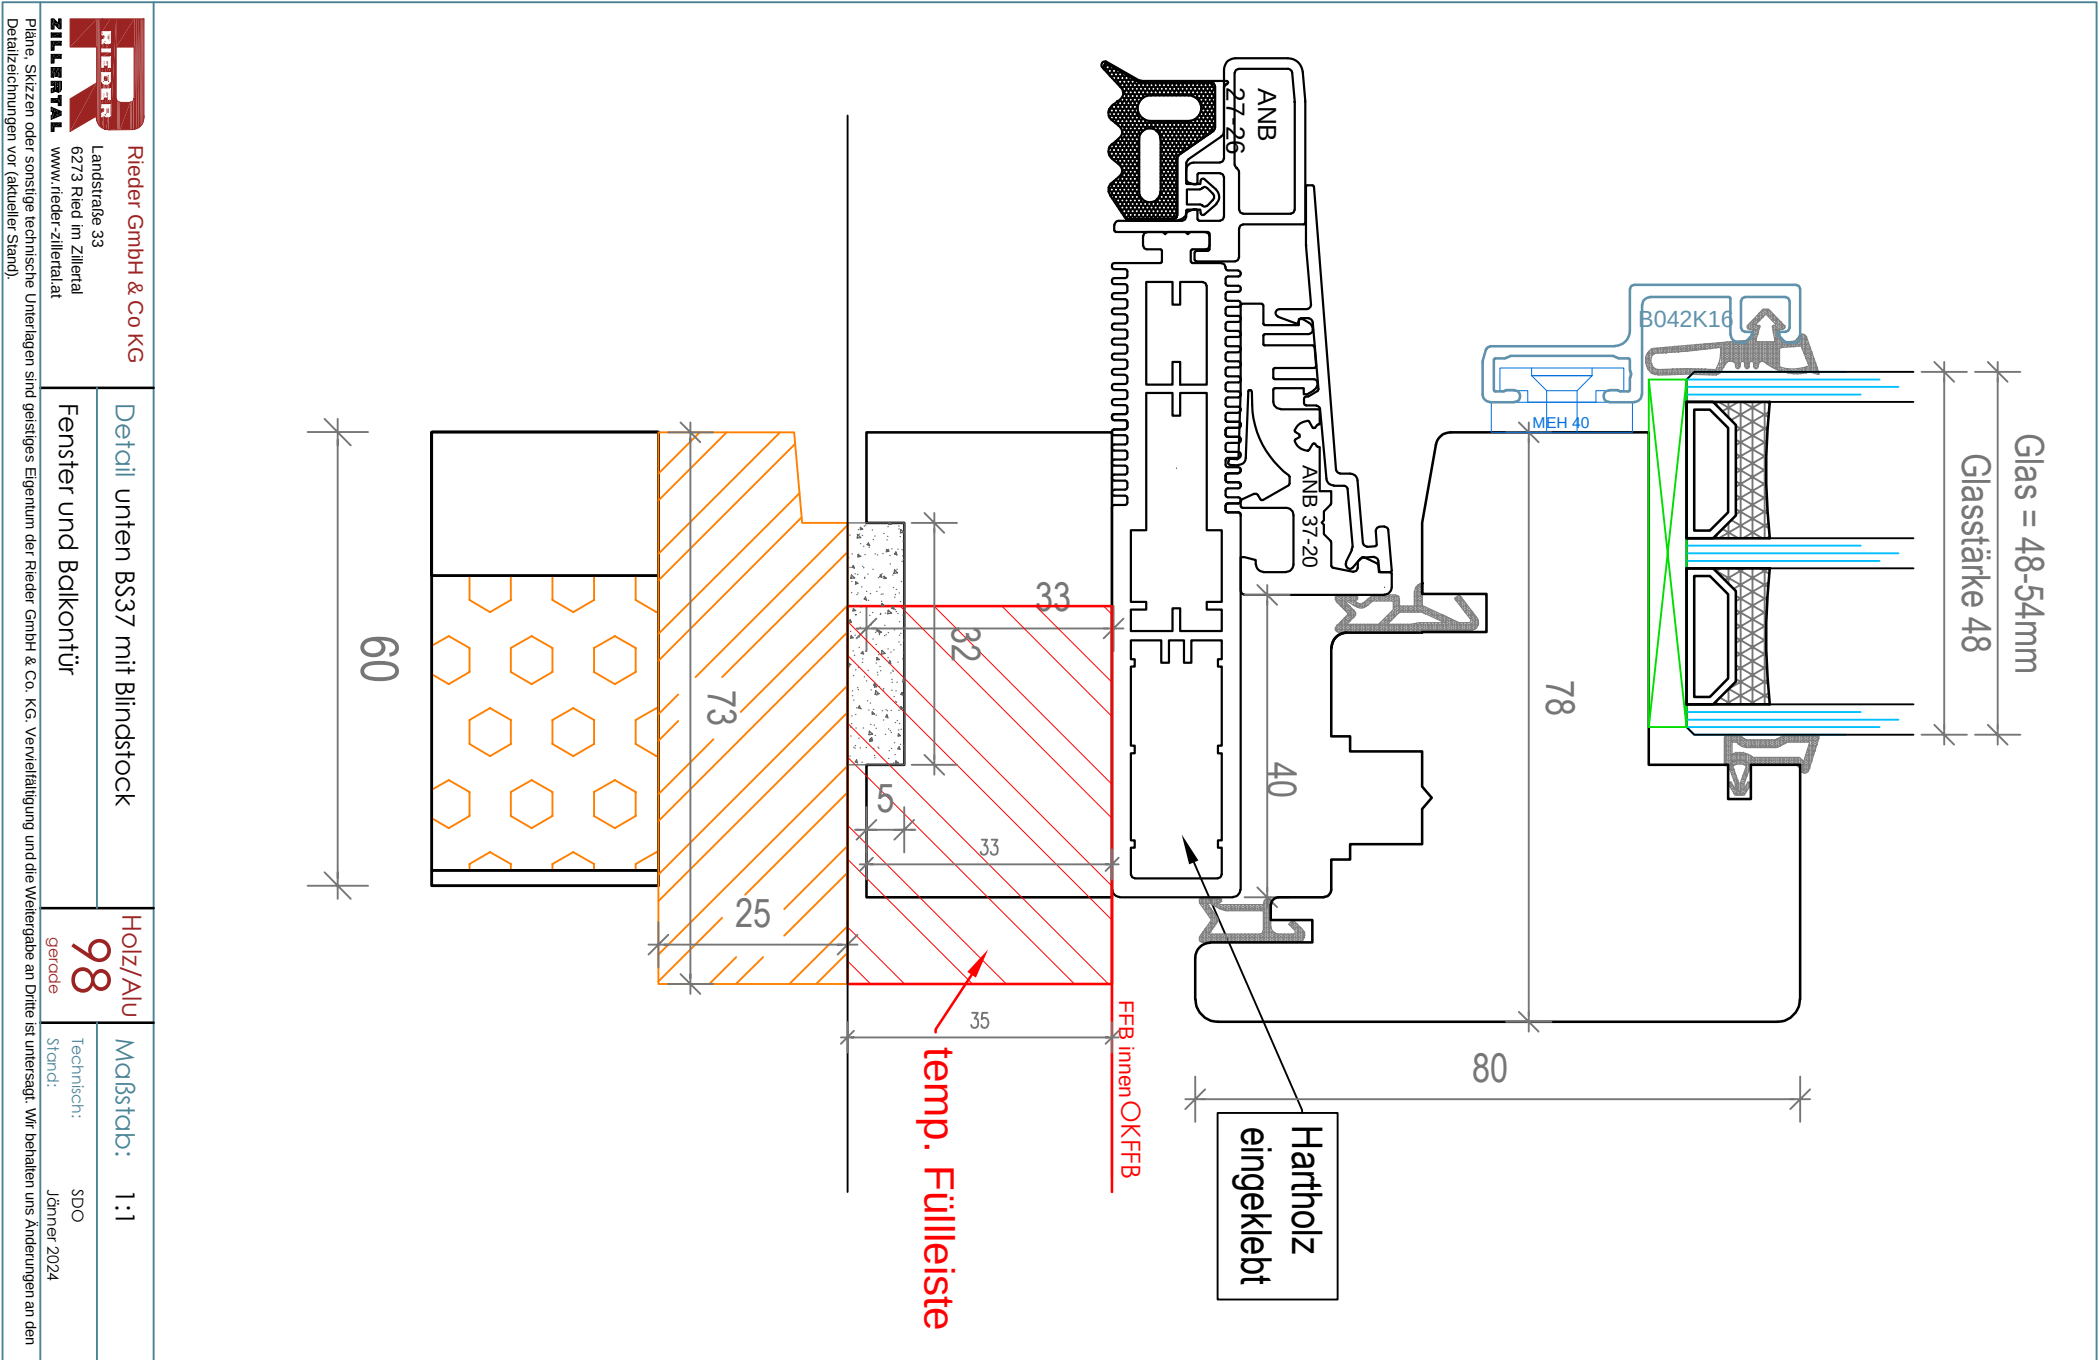

|   |                             |  |              |                                                             |
|---|-----------------------------|--|--------------|-------------------------------------------------------------|
|  <b>Rieder GmbH &amp; Co KG</b><br>Landstraße 33<br>6273 Ried im Zillertal<br>www.rieder-zillertal.at | Detail unten mit Blindstock |  | Holz/Alu     | Maßstab: 1:1<br><br>Technisch: SDO<br>Jänner 2024<br>Stand: |
|   | Fenster und Balkontür       |  | 98<br>gerade |                                                             |

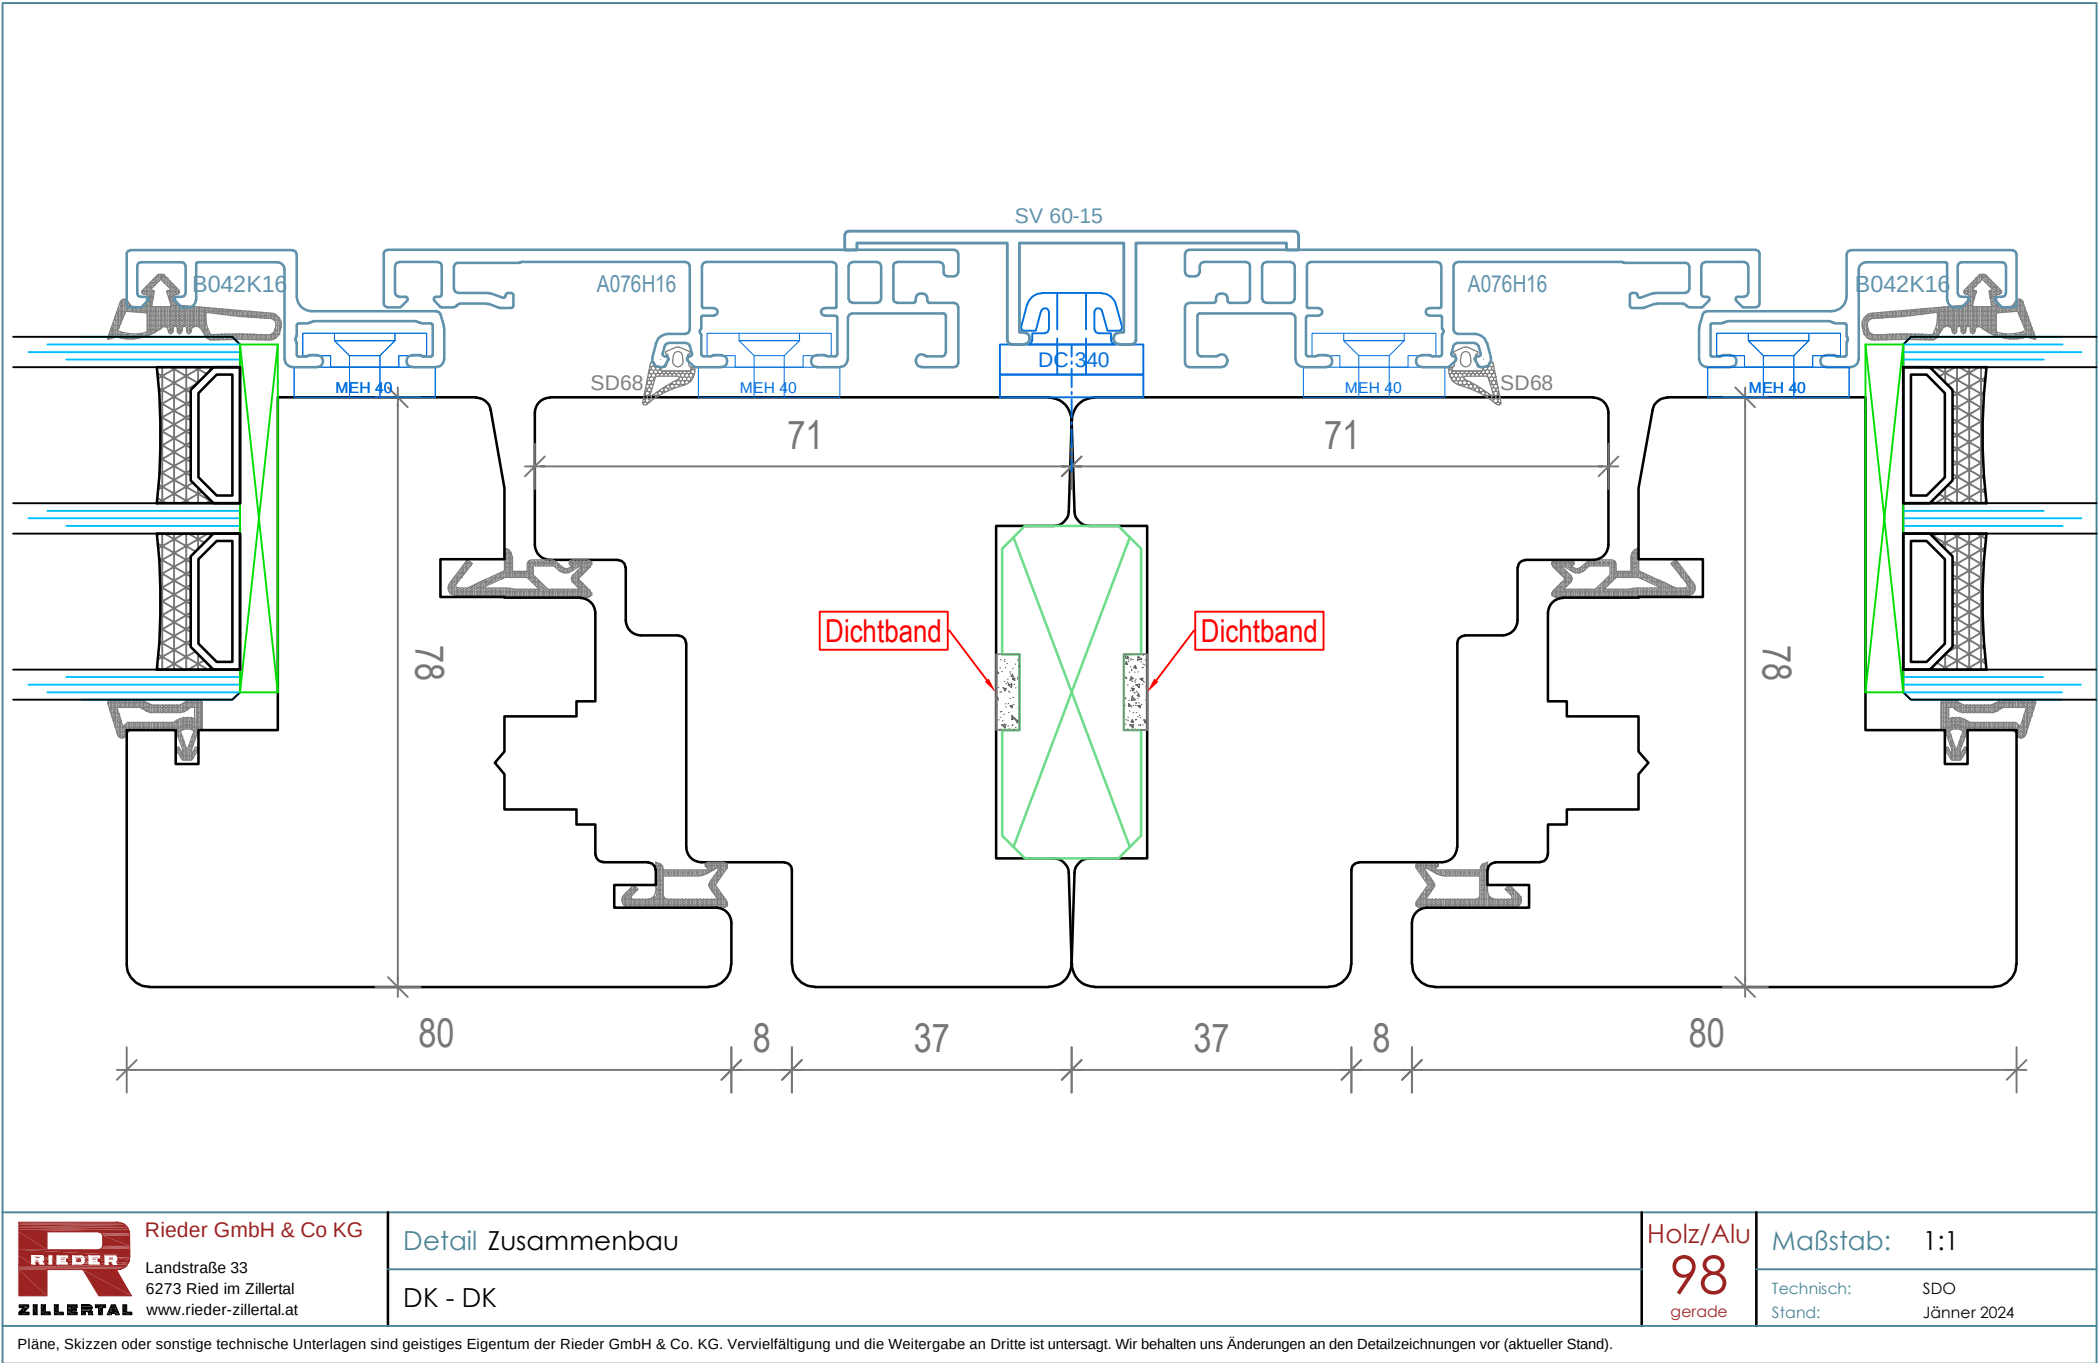

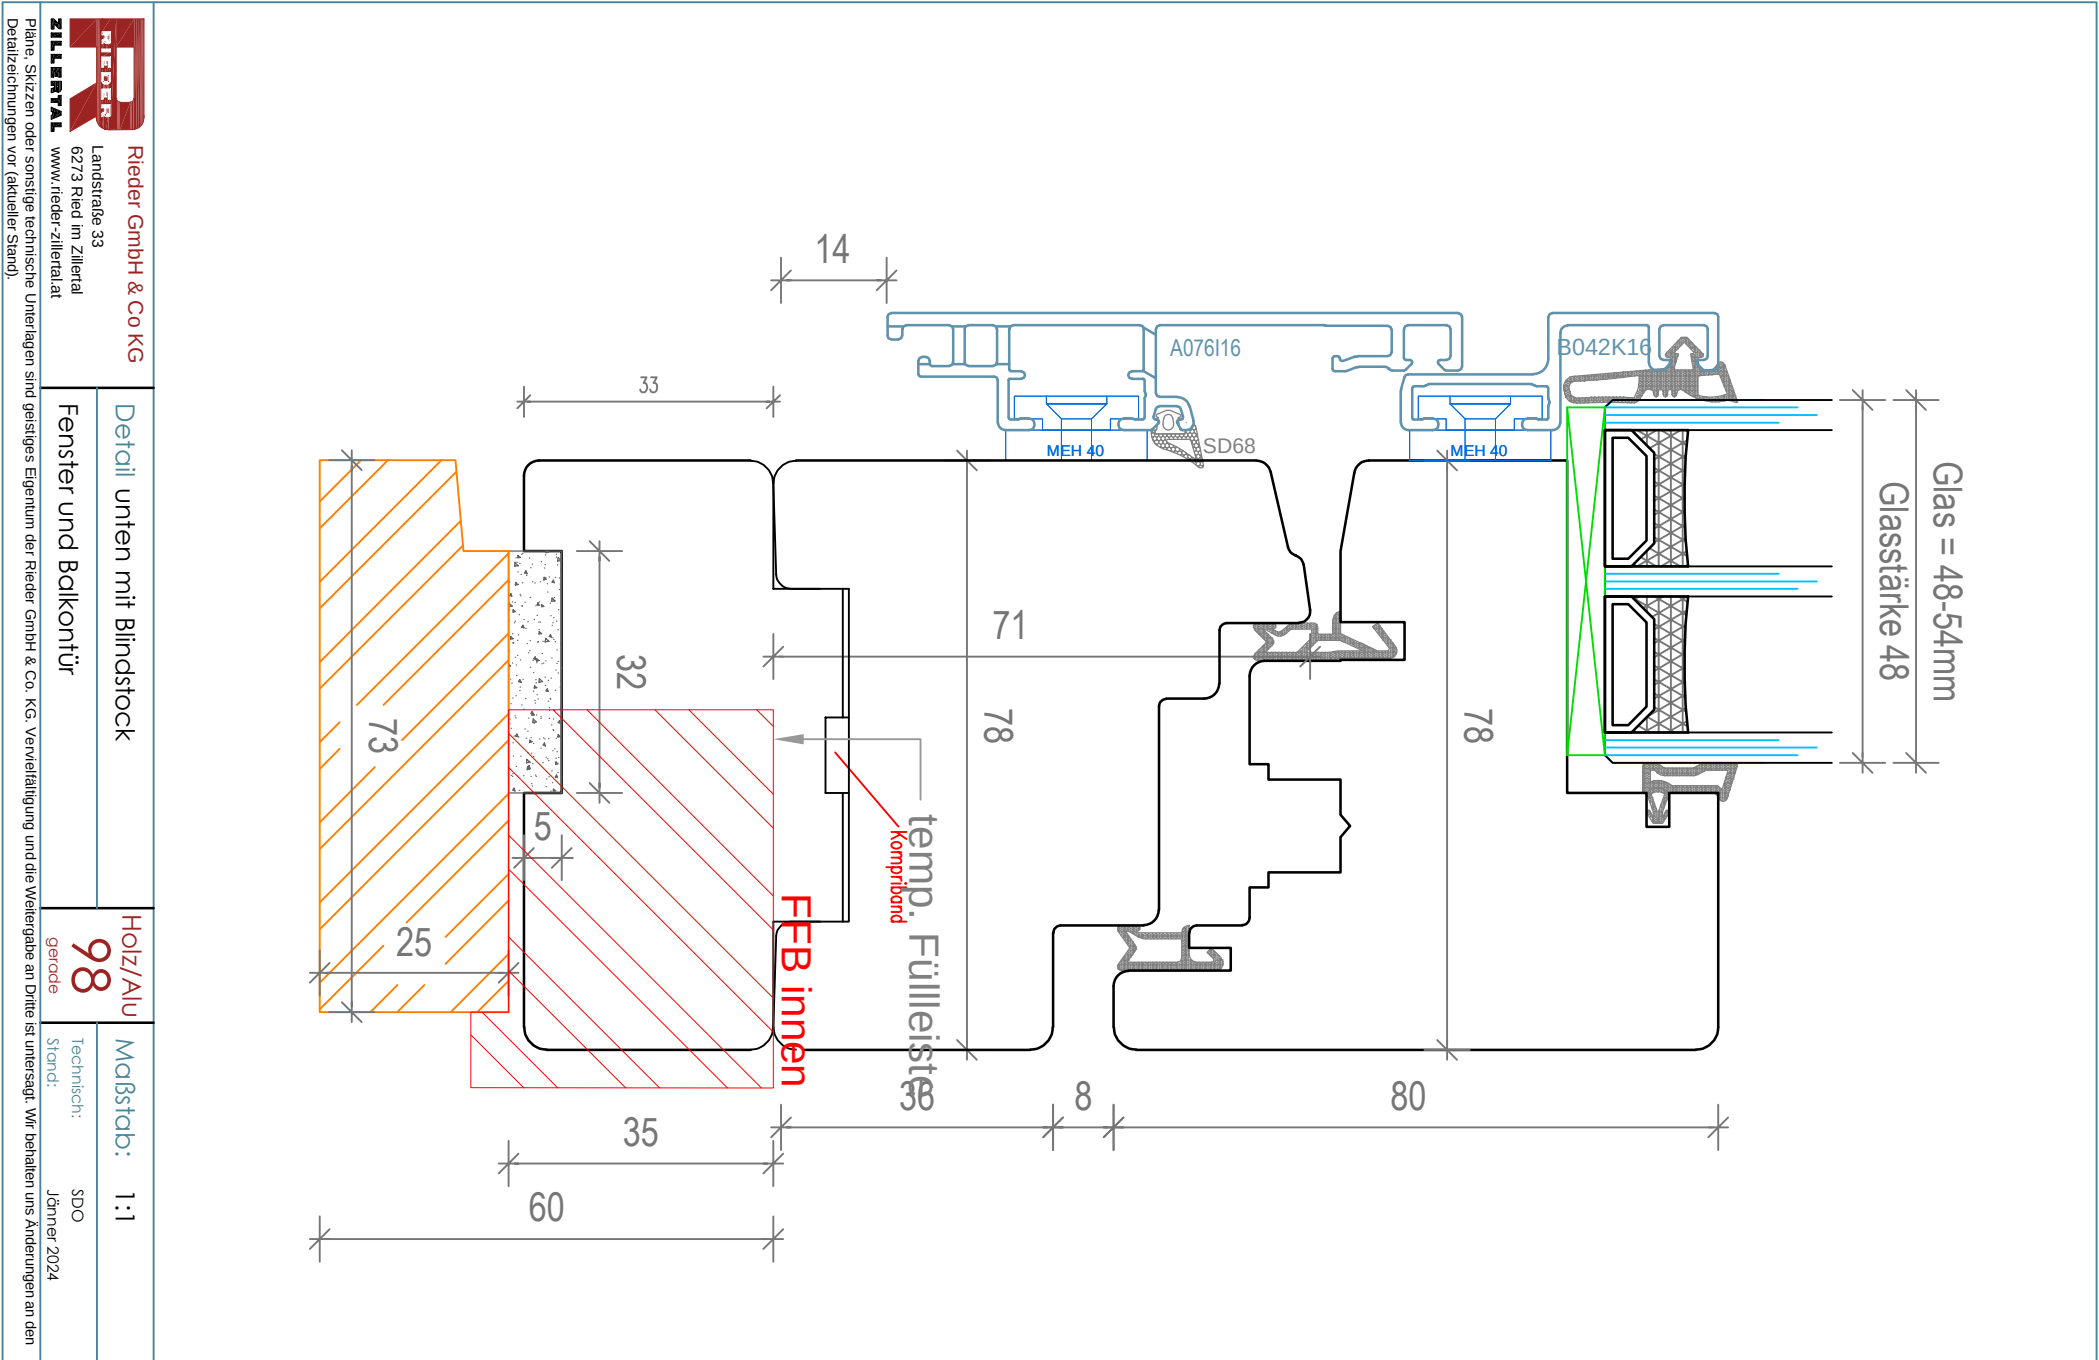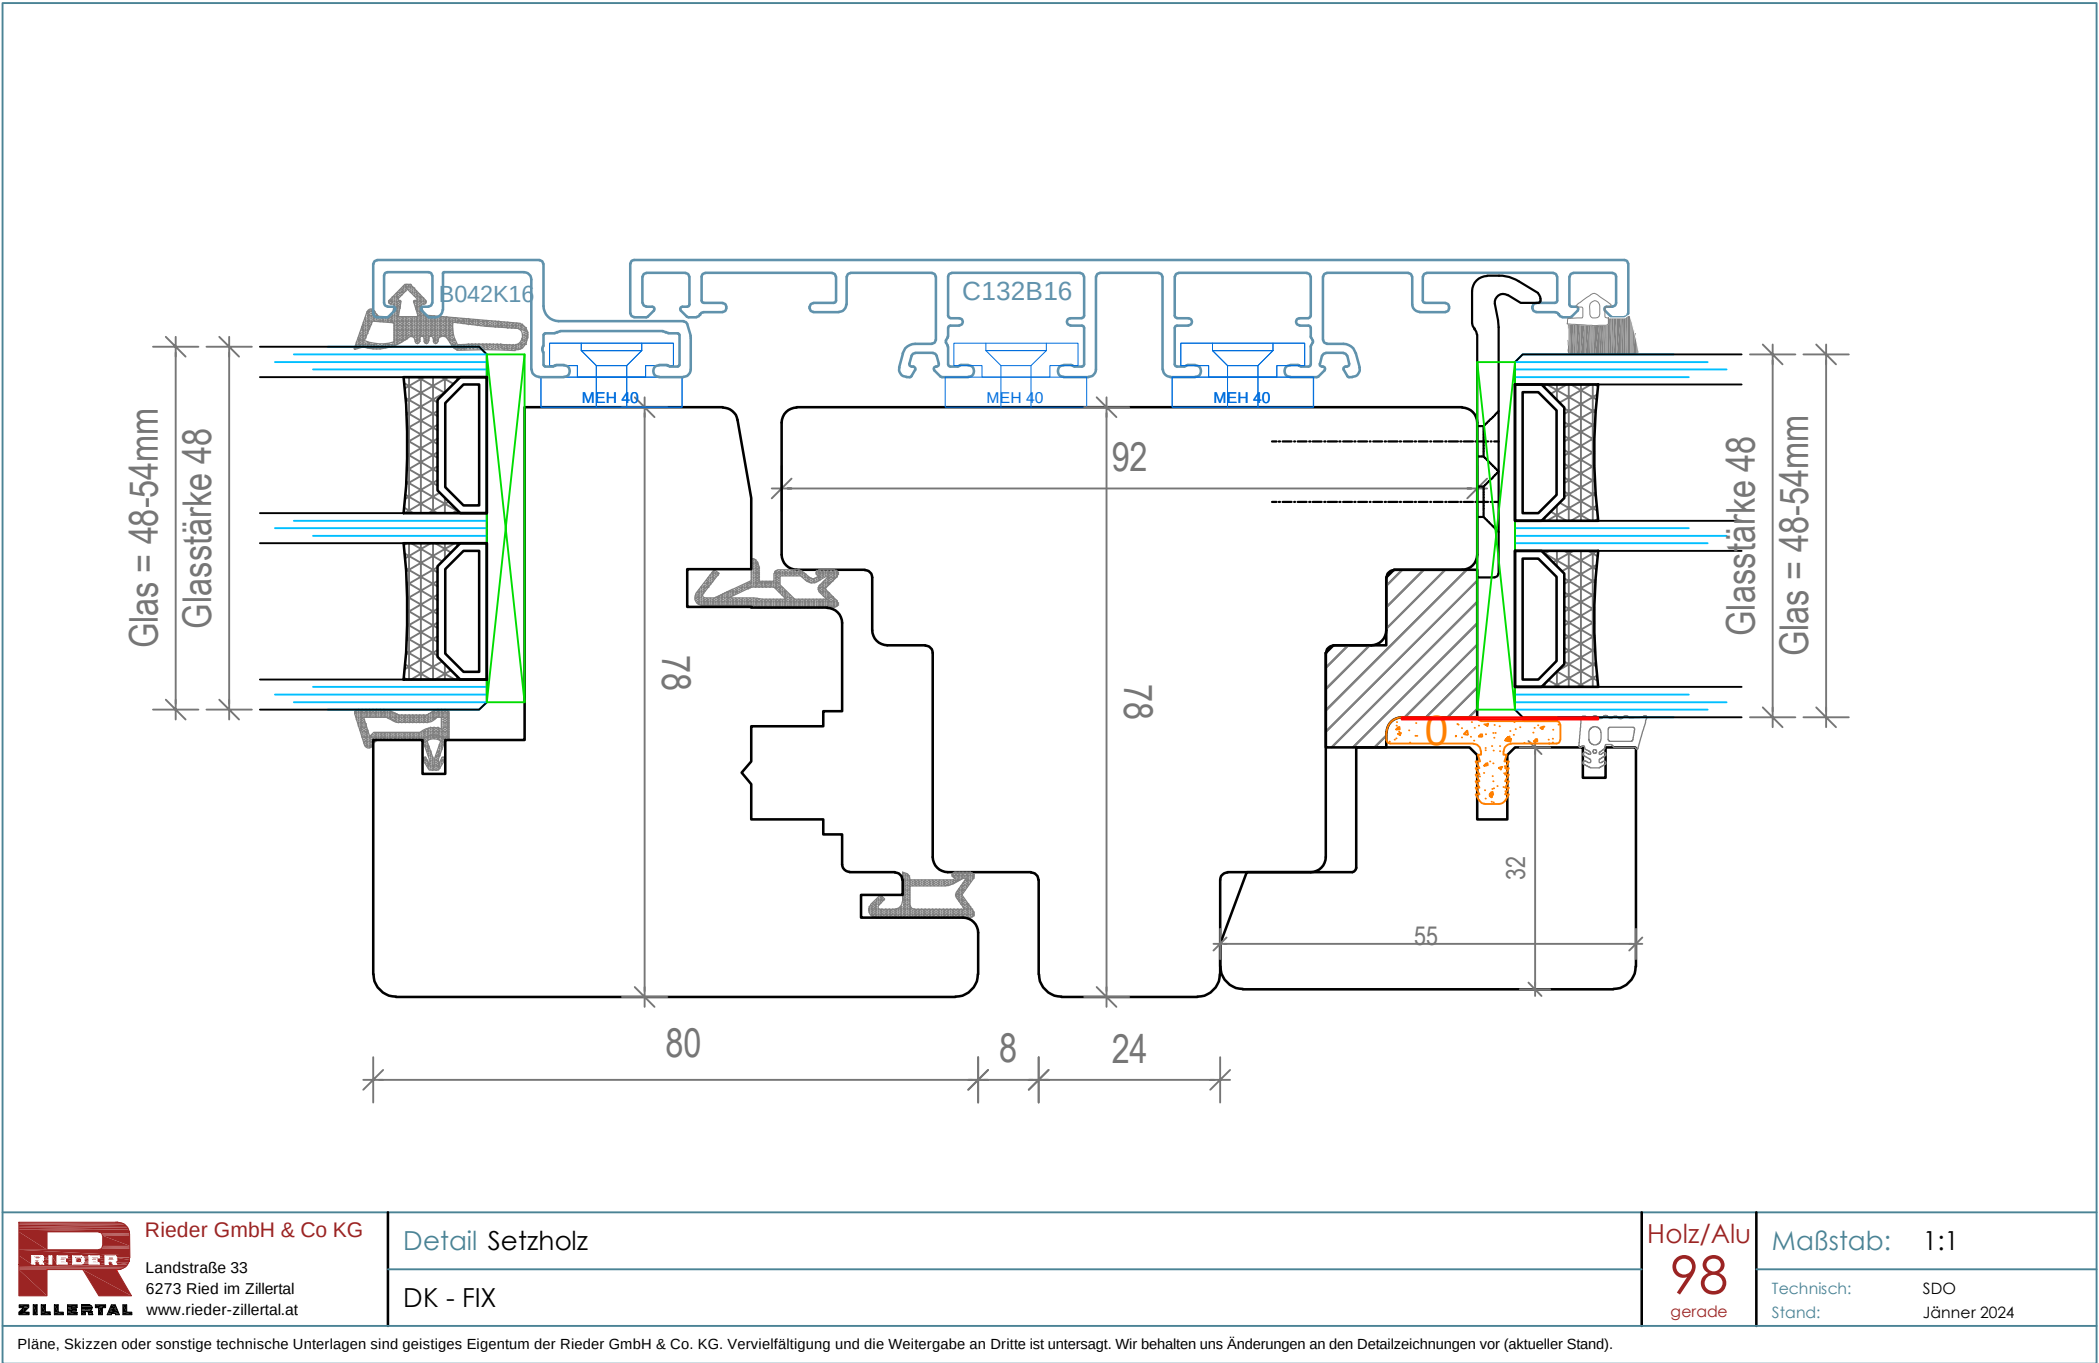

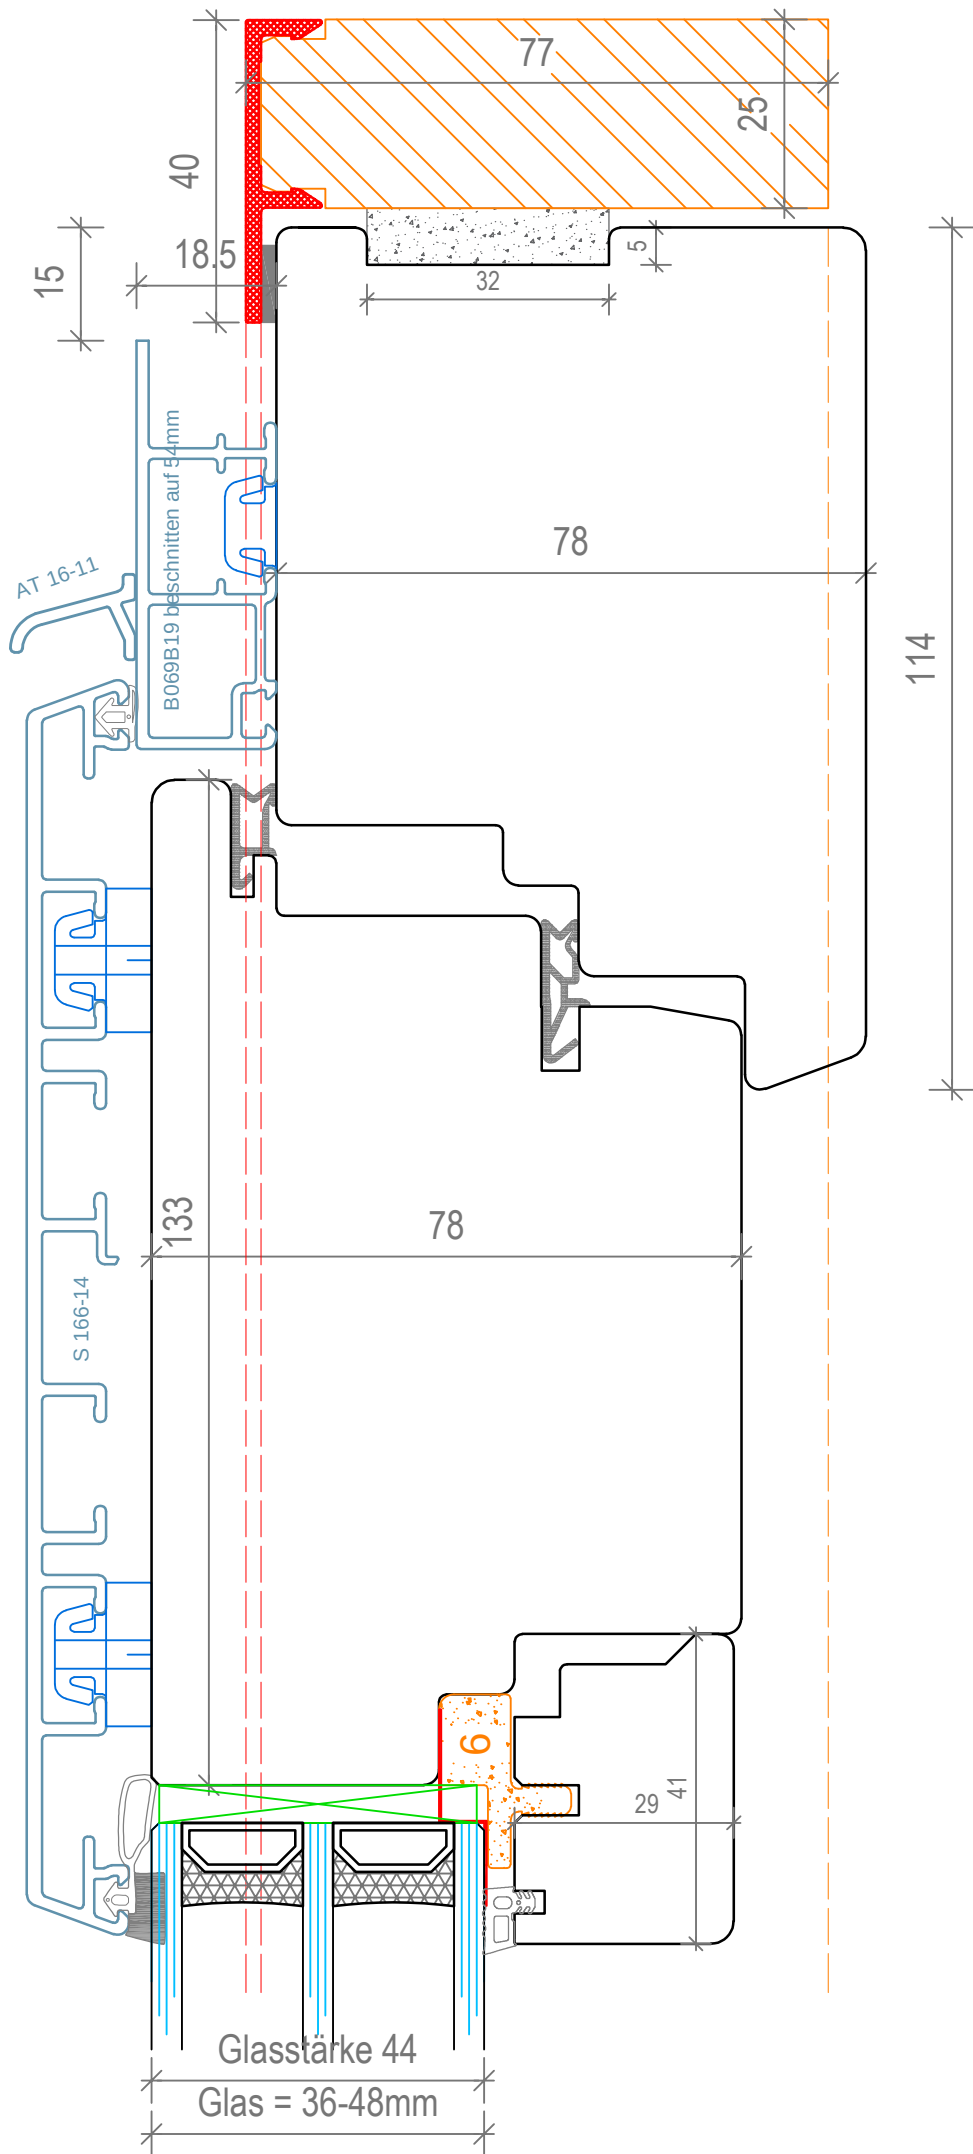

Rieder GmbH & Co KG  
Landstraße 33  
6273 Ried im Zillertal  
www.rieder-zillertal.at


Detail oben mit Blindstock

Nebeneingangstüre nach außen öffnend

Holz/Alu  
78  
gerade

Maßstab: 1:1

Technisch: SDO  
Stand: Jänner 2024

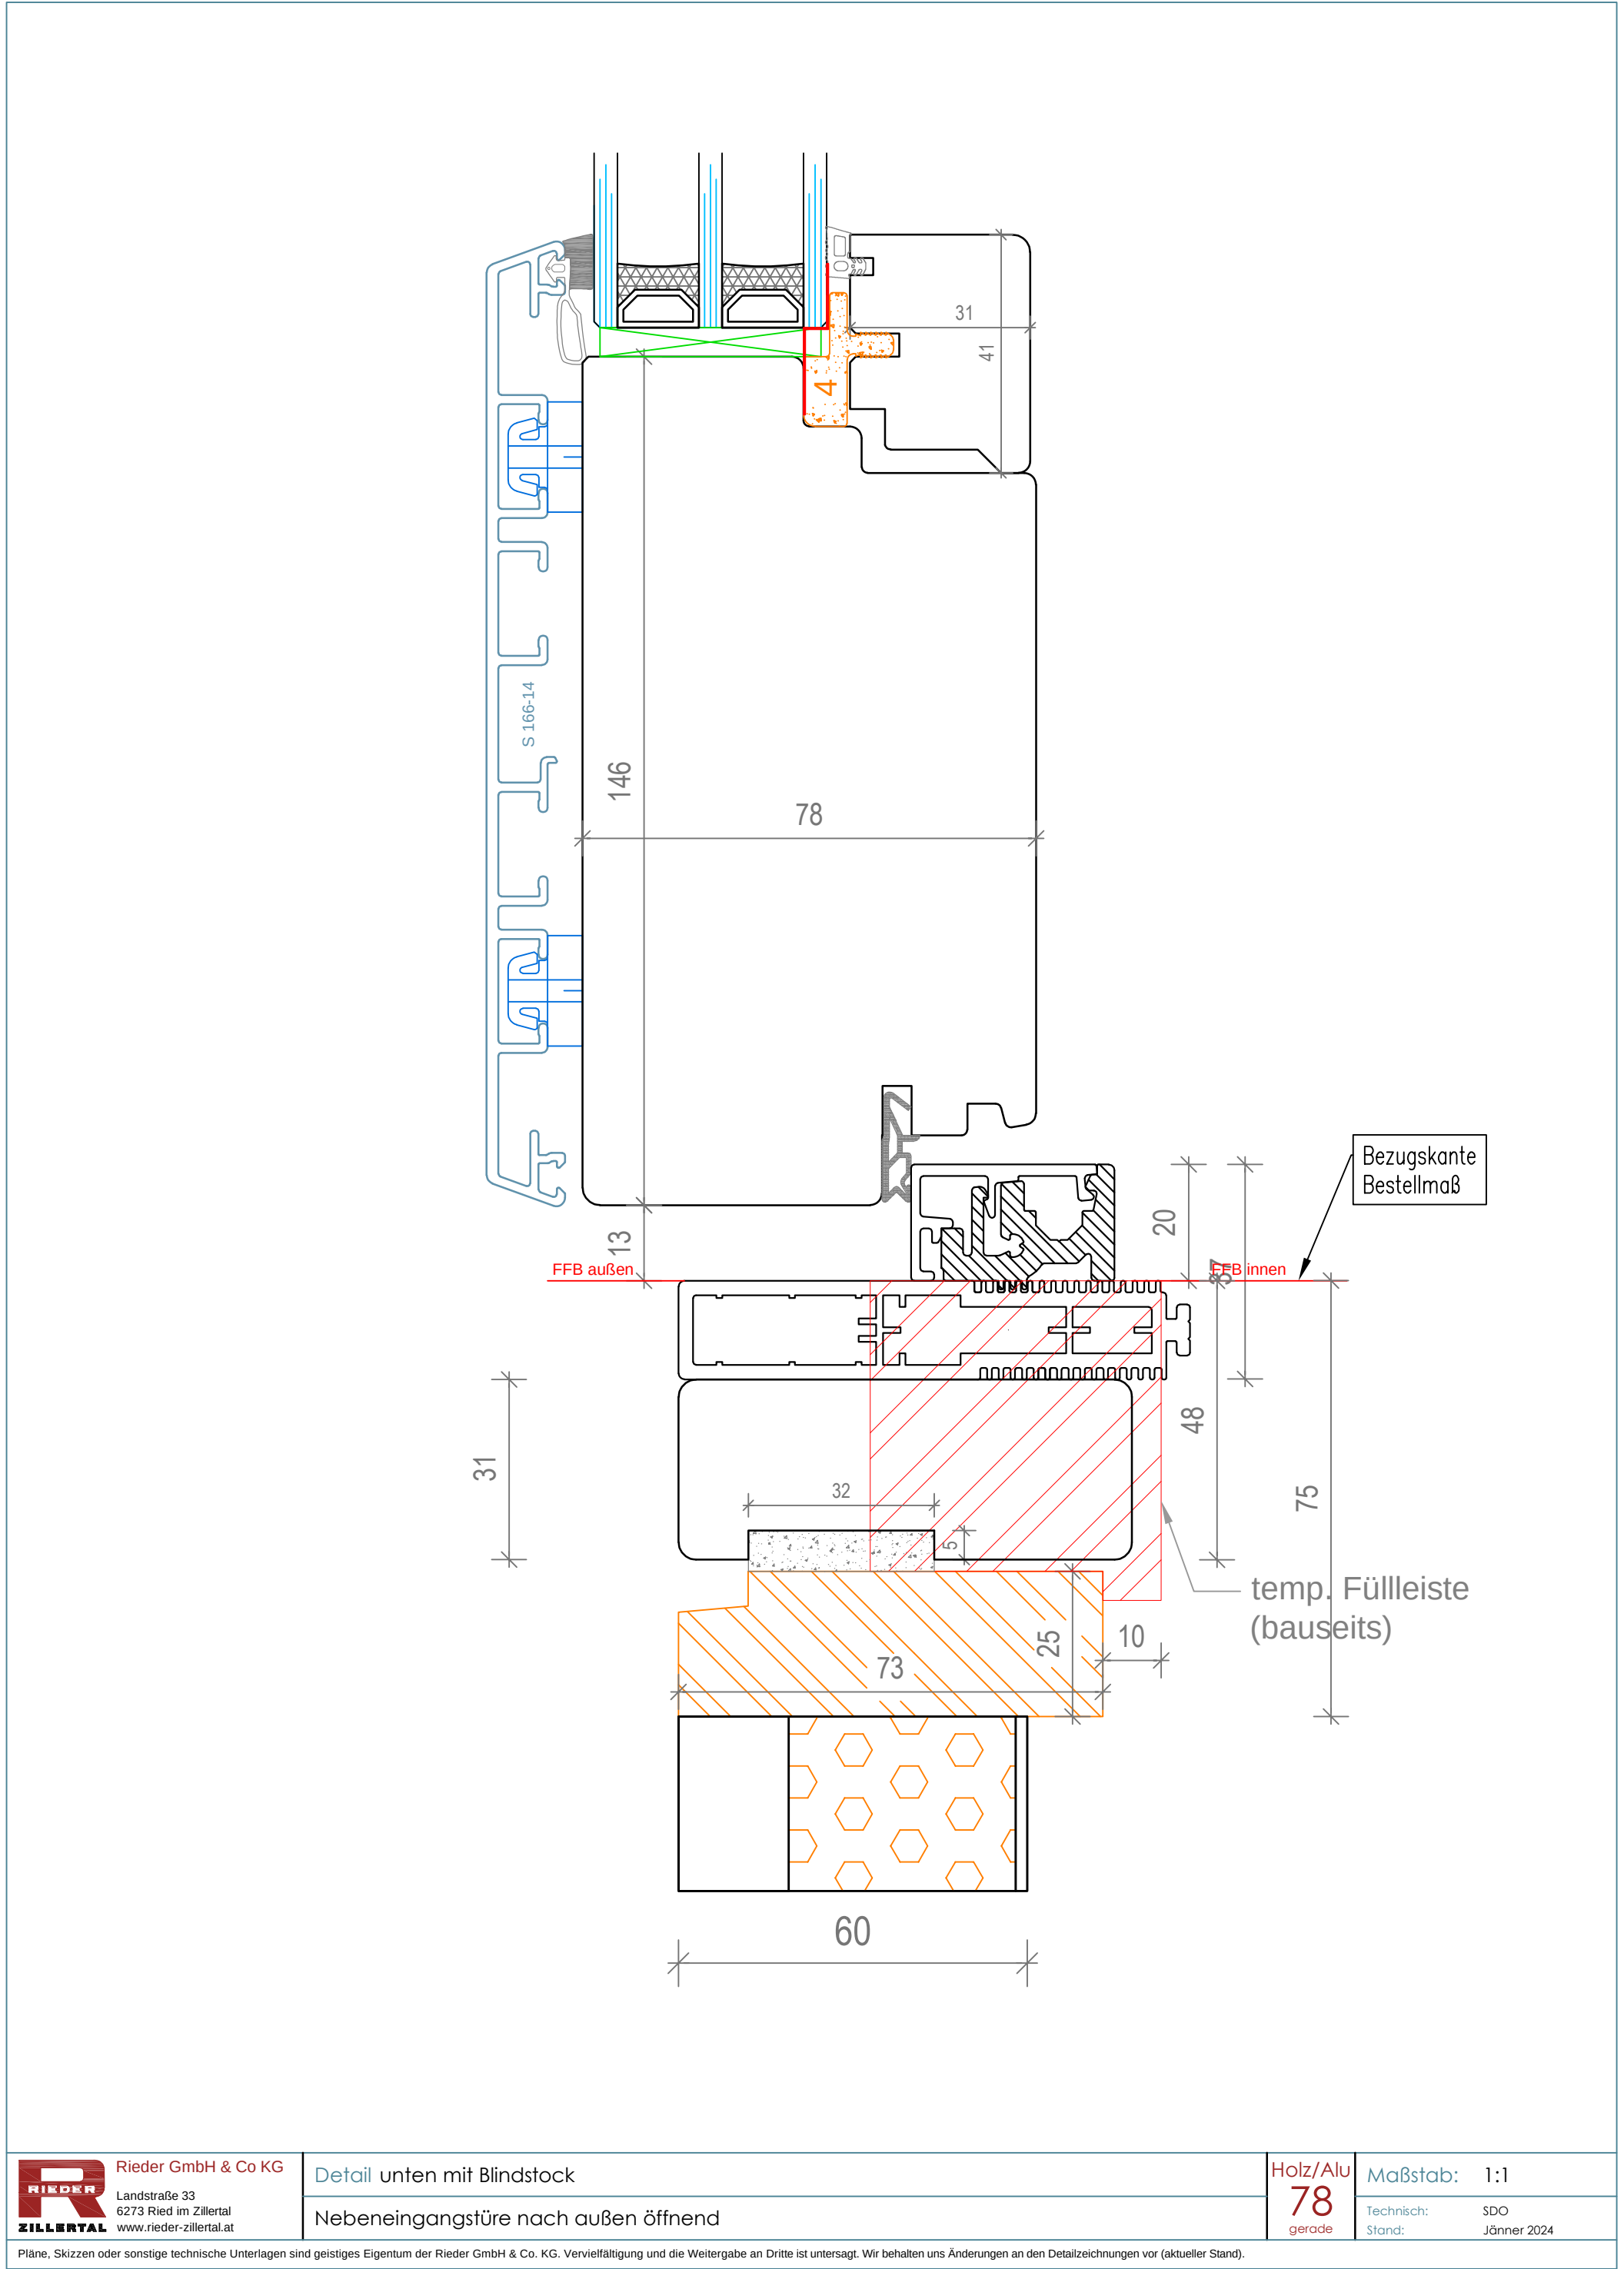

Rieder GmbH & Co KG  
Landstraße 33  
6273 Ried im Zillertal  
www.rieder-zillertal.at

Detail unten mit Blindstock

Nebeneingangstüre nach außen öffnend


Holz/Alu  
78  
gerade

Maßstab: 1:1

Technisch: SDO  
Stand: Jänner 2024





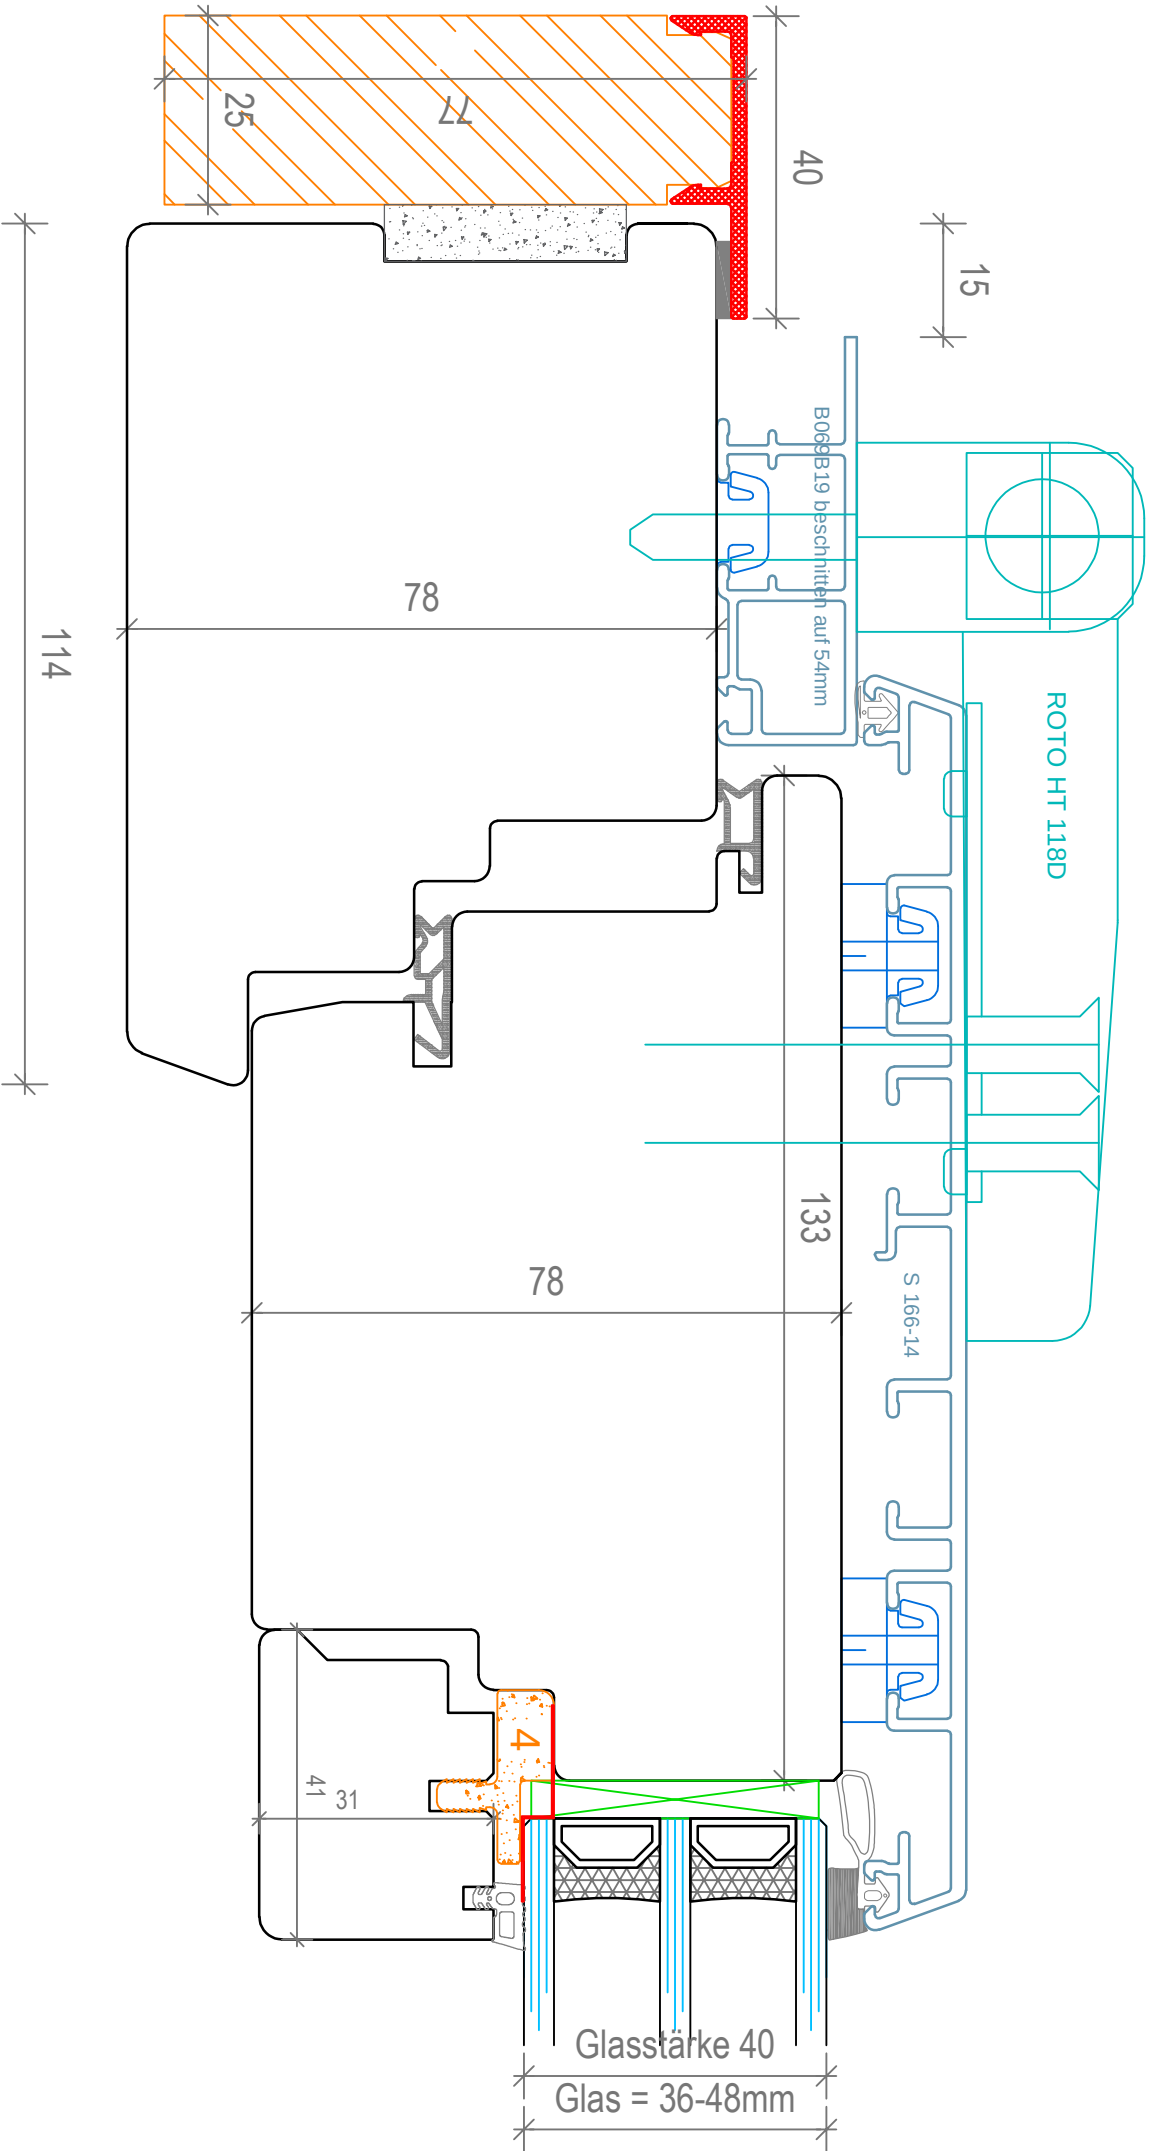

# Mit Verriegelung unten ist Standard

