


Elementübersicht

Seite: 1
Ried, am 15.07.2025
Druckzeit: 10:02:09

Auftragsnr.: 132475 HA
Kommission: Moonlight - Söll, zu 132207 + 132476
Kunde: Fenster, Türen, Parkett, Sonnenschutz SR.Schauraum GmbH
Fenstersystem: Rieder 98 HA Innen FB

Techniker: sdo
Vertreter: rch

Maßstab: 1:20	Gesamt Außenmaß: 1915,0 * 2180,0	Verbreiterungen:	Stück	Ansichtsbreite
Pos.: 1			1	33,0
Kunden Pos.: DG 03-05				Blindholz für PVC-Blindstock Universal
Stück: 1				

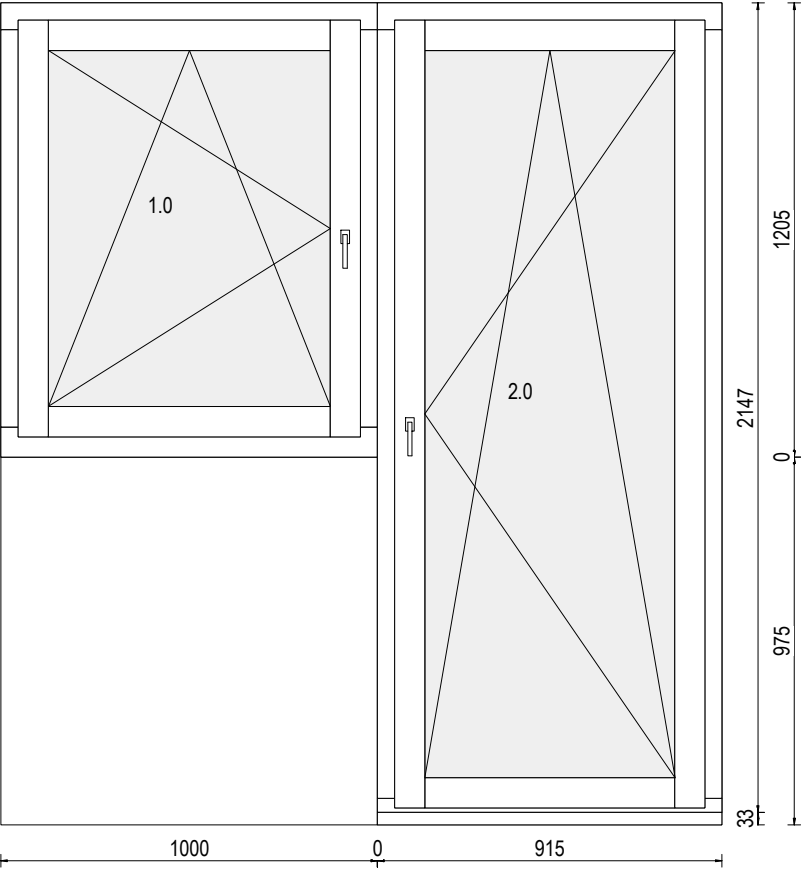

Elementübersicht

Seite: 2
Ried, am 15.07.2025
Druckzeit: 10:02:10

Auftragsnr.: 132475 HA

Techniker: sdo

Kommission: Moonlight - Söll, zu 132207 + 132476

Vertreter: rch

Kunde: Fenster, Türen, Parkett, Sonnenschutz SR.Schauraum GmbH

Fenstersystem: Rieder 98 HA Innen FB


Maßstab: 1:15

Gesamt Außenmaß: 815,0 * 1005,0

Pos.: 2

Kunden Pos.: DG 03-01

Stück: 1

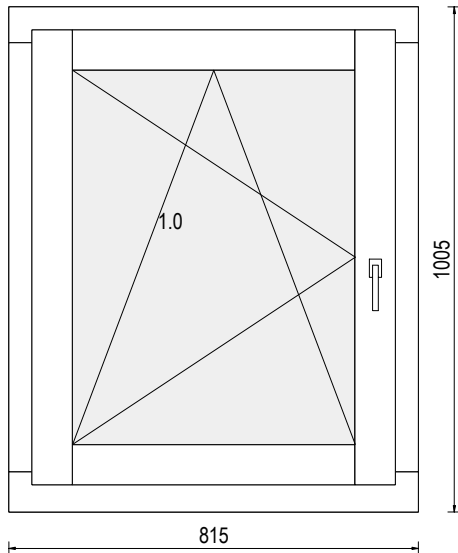


Elementübersicht

Auftragsnr.: 132475 HA
Kommission: Moonlight - Söll, zu 132207 + 132476
Kunde: Fenster, Türen, Parkett, Sonnenschutz SR.Schauraum GmbH
Fenstersystem: Rieder 98 HA Innen FB

Techniker: sdo
Vertreter: rch

Maßstab: 1:20	Gesamt Außenmaß: 1915,0 * 2180,0	Verbreiterungen:	Stück	Ansichtsbreite
Pos.: 3			1	33,0
Kunden Pos.: DG 03-05				Blindholz für PVC-Blindstock Universal
Stück: 1				

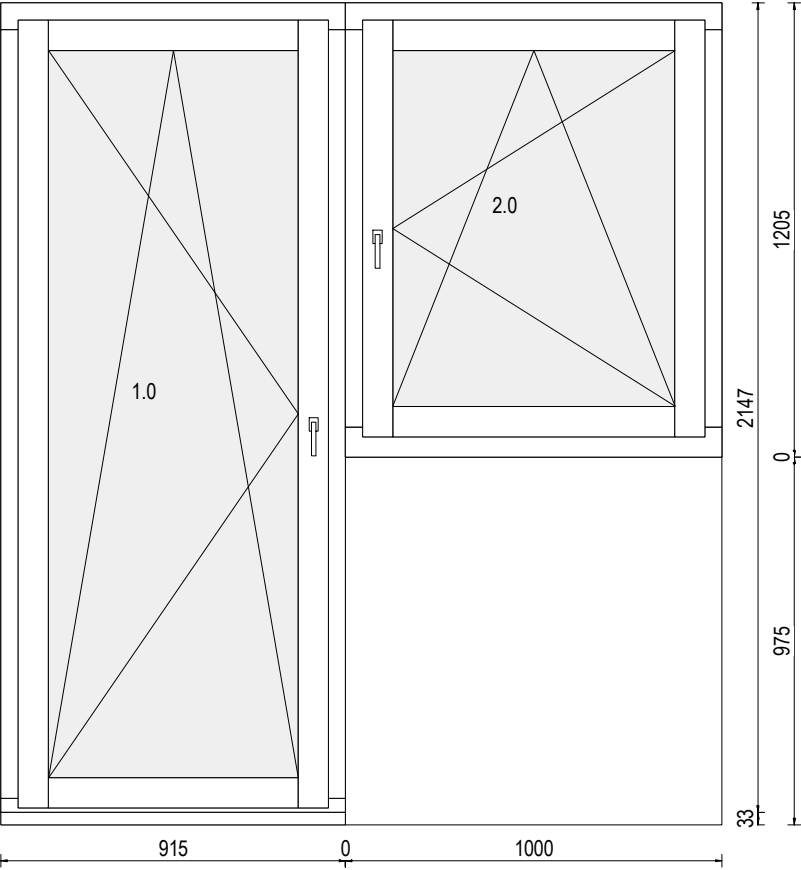


Elementübersicht

Auftragsnr.: 132475 HA
Kommission: Moonlight - Söll, zu 132207 + 132476
Kunde: Fenster, Türen, Parkett, Sonnenschutz SR.Schauraum GmbH
Fenstersystem: Rieder 98 HA Innen FB

Techniker: sdo
Vertreter: rch

Maßstab: 1:20	Gesamt Außenmaß: 1915,0 * 2181,0	Verbreiterungen:	Stück	Ansichtsbreite
Pos.: 4			2	33,0
Kunden Pos.: DG 03-03				Blindholz für PVC-Blindstock Universal
Stück: 1				

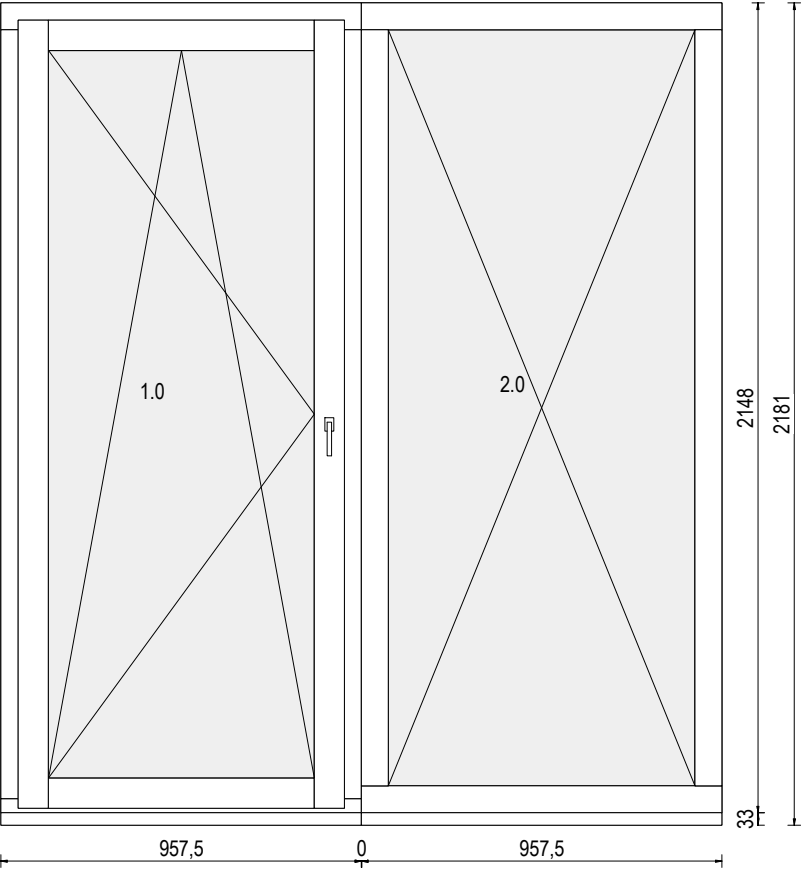

Elementübersicht

Seite: 5
Ried, am 15.07.2025
Druckzeit: 10:02:13

Auftragsnr.: 132475 HA

Kommission: Moonlight - Söll, zu 132207 + 132476


Kunde: Fenster, Türen, Parkett, Sonnenschutz SR.Schauraum GmbH

Fenstersystem: Rieder 98 HA Innen FB


Techniker: sdo

Vertreter: rch

Maßstab: 1:15 **Gesamt Außenmaß: 915,0 * 1205,0**
Pos.: 5
Kunden Pos.: DG 03-01
Stück: 1

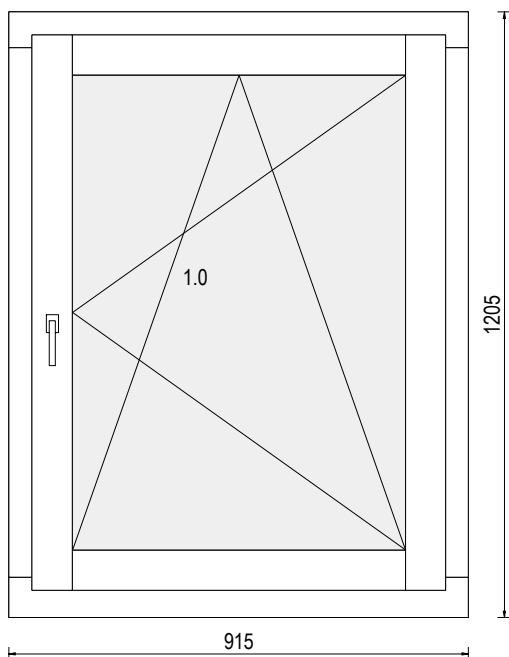

Maßstab: 1:30 **Gesamt Außenmaß: 3025,0 * 1205,0**
Pos.: 6
Kunden Pos.: DG 03-09
Stück: 1

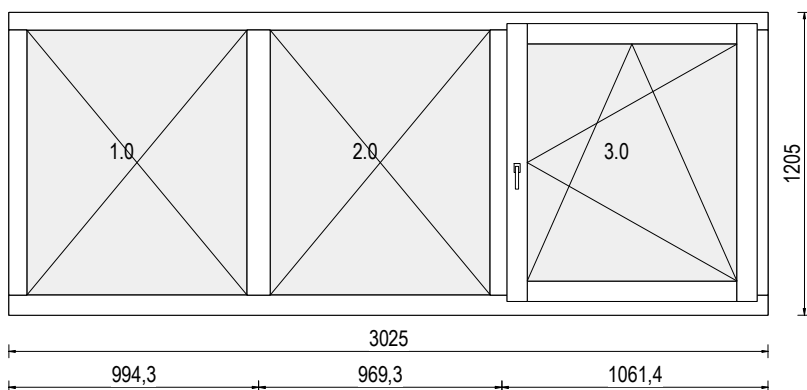

Elementübersicht

Seite: 6
Ried, am 15.07.2025
Druckzeit: 10:02:15

Auftragsnr.: 132475 HA

Techniker: sdo

Kommission: Moonlight - Söll, zu 132207 + 132476

Vertreter: rch

Kunde: Fenster, Türen, Parkett, Sonnenschutz SR.Schauraum GmbH

Fenstersystem: Rieder 98 HA Innen FB


Maßstab: 1:15

Gesamt Außenmaß: 1420,0 * 1205,0

Pos.: 7

Kunden Pos.: DG 03-08

Stück: 1

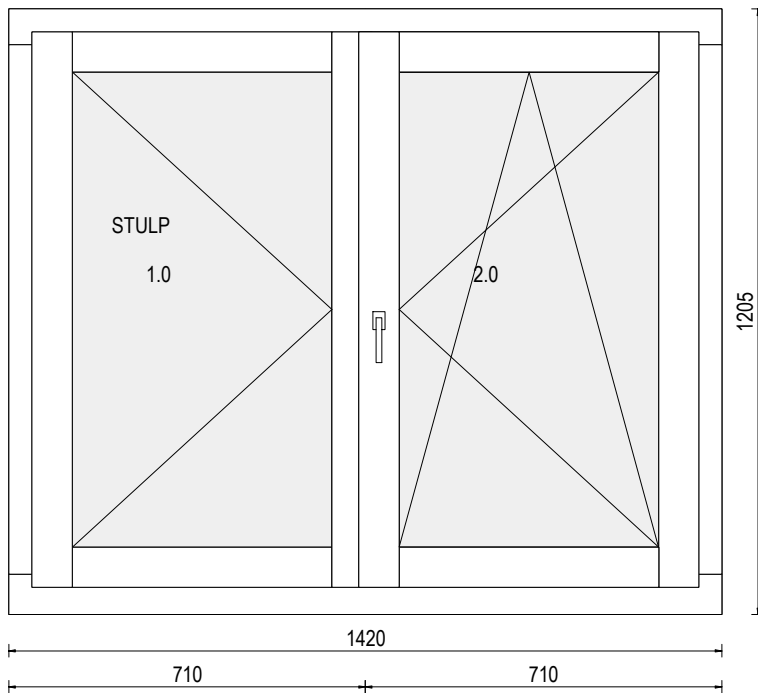


Elementübersicht

Seite: 7
Ried, am 15.07.2025
Druckzeit: 10:02:15

Auftragsnr.: 132475 HA	Techniker: sdo
Kommission: Moonlight - Söll, zu 132207 + 132476	Vertreter: rch
Kunde: Fenster, Türen, Parkett, Sonnenschutz SR.Schauraum GmbH	
Fenstersystem: Rieder 98 HA Innen FB	

Maßstab: 1:20	Gesamt Außenmaß: 1115,0 * 2181,0	Verbreiterungen:	Stück	Ansichtsbreite
Pos.: 8			1	33,0
Kunden Pos.: DG 03-02				Blindholz für PVC-Blindstock Universal
Stück: 1				

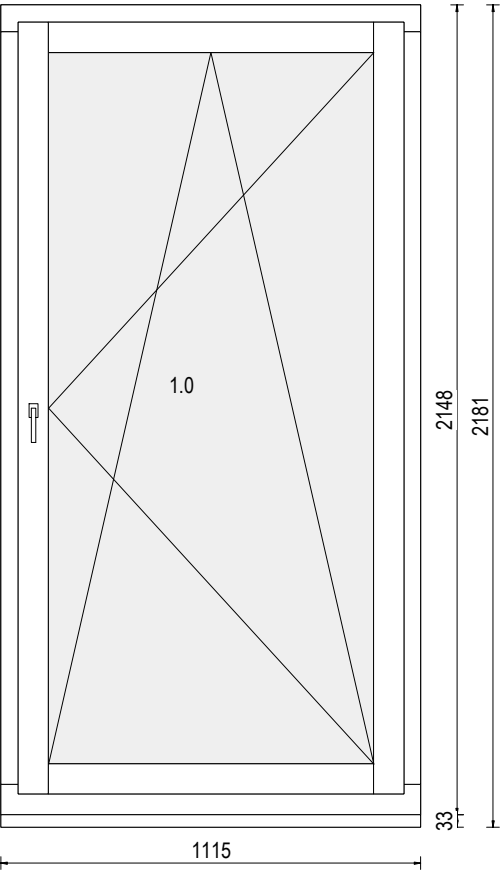

Elementübersicht

Seite: 8
Ried, am 15.07.2025
Druckzeit: 10:02:16

Auftragsnr.: 132475 HA

Kommission: Moonlight - Söll, zu 132207 + 132476

Kunde: Fenster, Türen, Parkett, Sonnenschutz SR.Schauraum GmbH


Fenstersystem: Rieder 98 HA Innen FB

Techniker: sdo

Vertreter: rch


Maßstab: 1:15
Pos.: 9
Kunden Pos.: DG 03-08
Stück: 1

Gesamt Außenmaß: 1420,0 * 1205,0

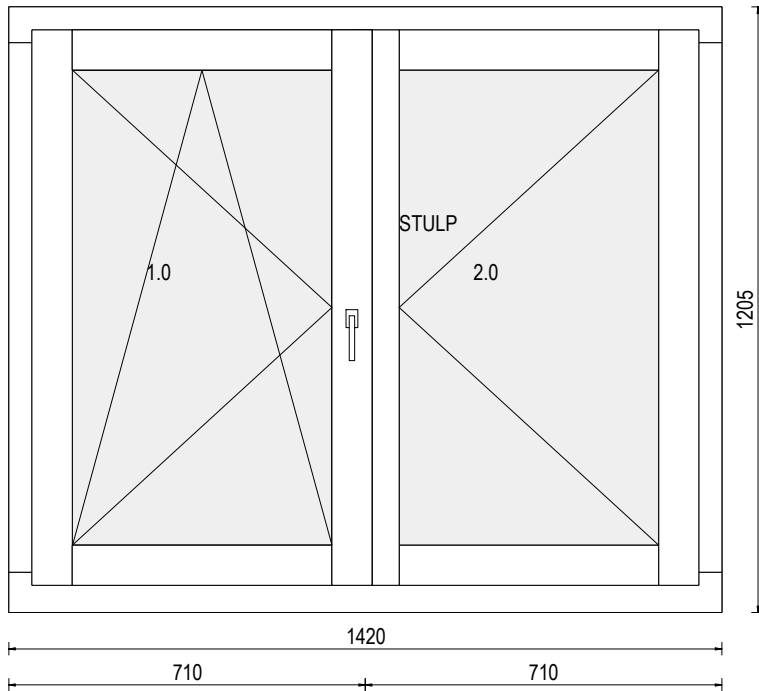

Maßstab: 1:20
Pos.: 10
Kunden Pos.: DG 03-04
Stück: 1

Gesamt Außenmaß: 2720,0 * 1205,0

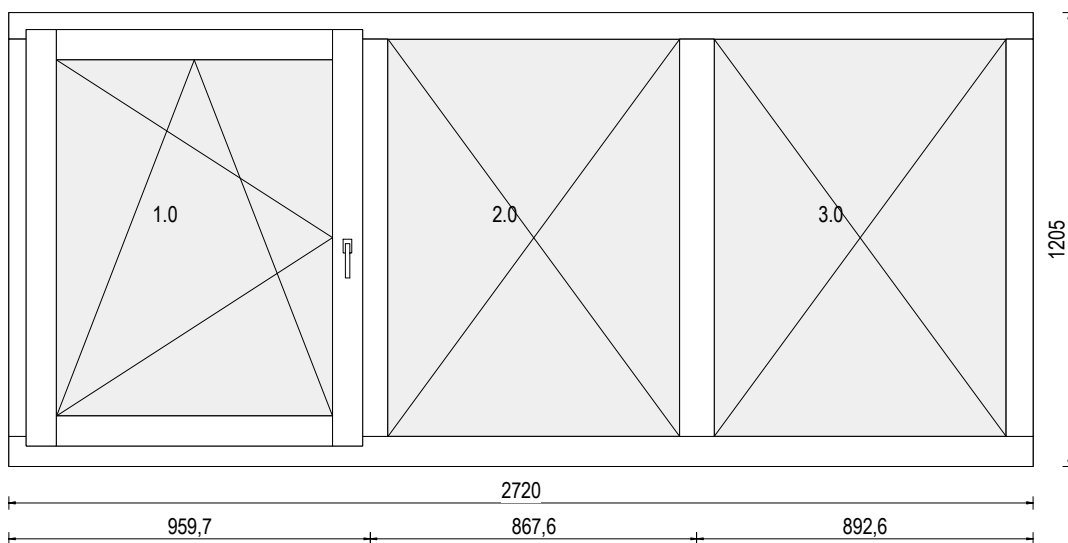


Elementübersicht

Auftragsnr.: 132475 HA
Kommission: Moonlight - Söll, zu 132207 + 132476
Kunde: Fenster, Türen, Parkett, Sonnenschutz SR.Schauraum GmbH
Fenstersystem: Rieder 98 HA Innen FB

Techniker: sdo
Vertreter: rch

Maßstab: 1:20	Gesamt Außenmaß: 1915,0 * 2180,0	Verbreiterungen:	Stück	Ansichtsbreite
Pos.: 11			1	33,0
Kunden Pos.: DG 03-05				Blindholz für PVC-Blindstock Universal
Stück: 1				

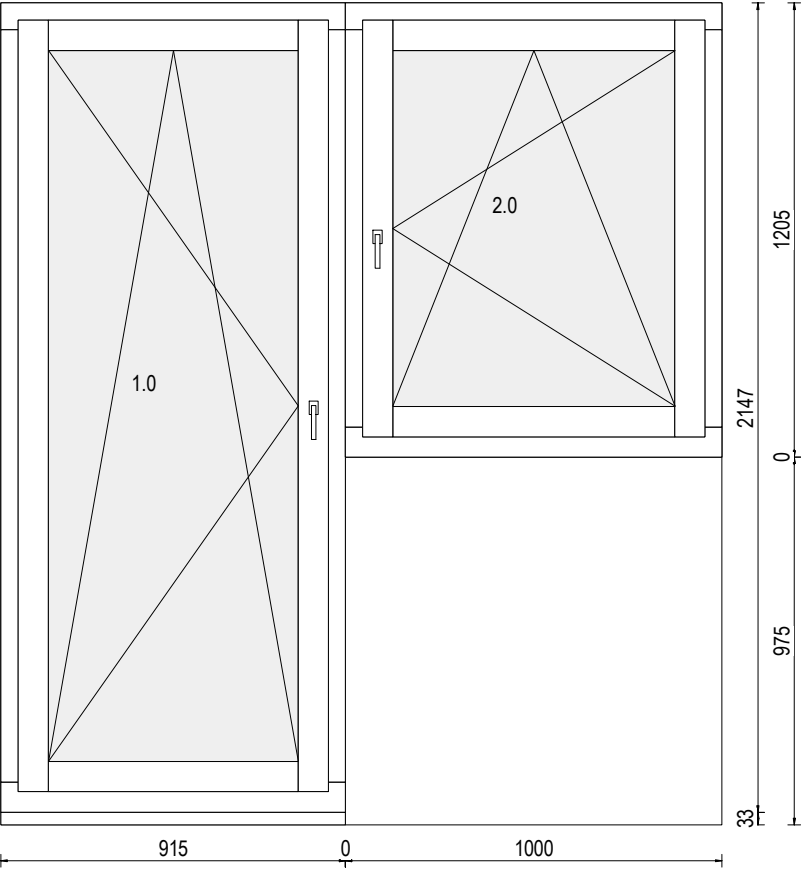


Elementübersicht

Auftragsnr.: 132475 HA
Kommission: Moonlight - Söll, zu 132207 + 132476
Kunde: Fenster, Türen, Parkett, Sonnenschutz SR.Schauraum GmbH
Fenstersystem: Rieder 98 HA Innen FB

Techniker: sdo
Vertreter: rch

Maßstab: 1:20	Gesamt Außenmaß: 1915,0 * 2181,0	Verbreiterungen:	Stück	Ansichtsbreite
Pos.: 12			2	33,0
Kunden Pos.: DG 03-03				Blindholz für PVC-Blindstock Universal
Stück: 1				

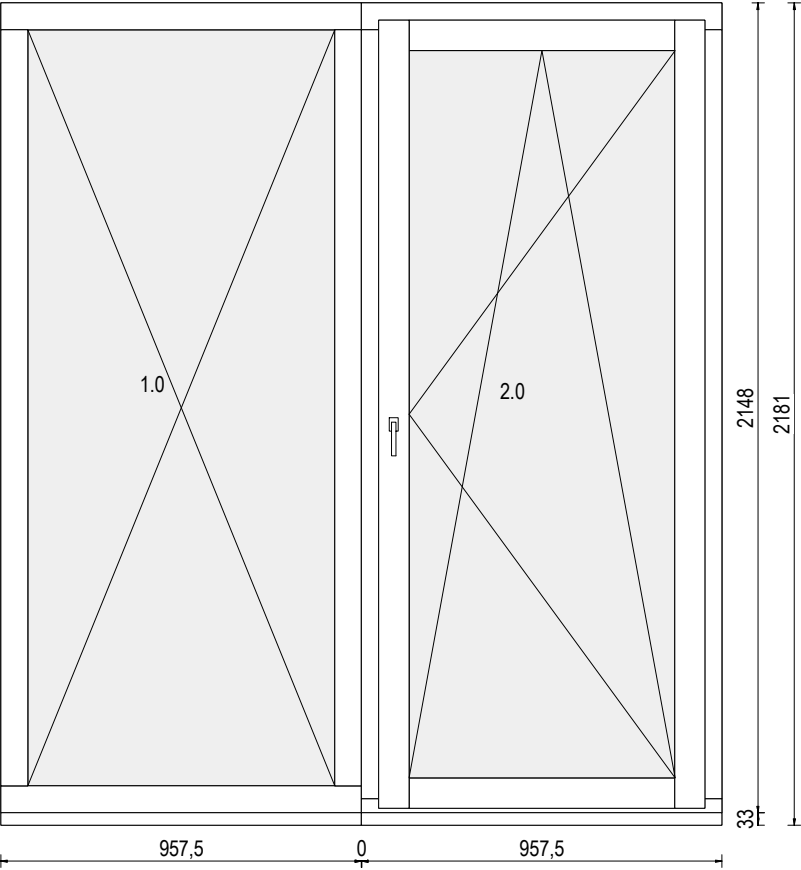

Auftragsnr.: 132475 HA

Techniker: sdo

Kommission: Moonlight - Söll, zu 132207 + 132476

Vertreter: rch

Kunde: Fenster, Türen, Parkett, Sonnenschutz SR.Schauraum GmbH

Fenstersystem: Rieder 98 HA Innen FB


Maßstab: 1:15

Gesamt Außenmaß: 665,0 * 1205,0

Pos.: 13

Kunden Pos.: DG 03-01

Stück: 1

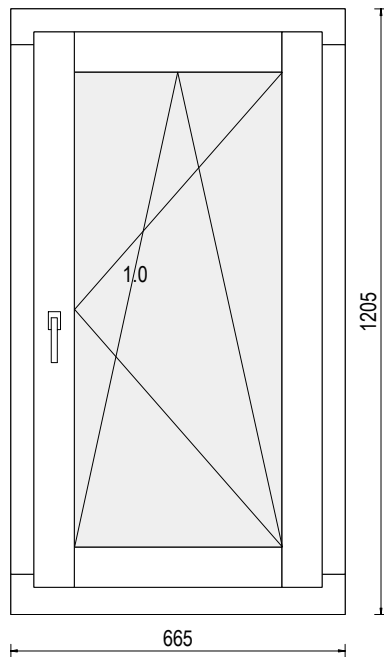


Elementübersicht

Auftragsnr.: 132475 HA
Kommission: Moonlight - Söll, zu 132207 + 132476
Kunde: Fenster, Türen, Parkett, Sonnenschutz SR.Schauraum GmbH
Fenstersystem: Rieder 98 HA Innen FB

Techniker: sdo
Vertreter: rch

Maßstab: 1:20	Gesamt Außenmaß: 1915,0 * 2181,0	Verbreiterungen:	Stück	Ansichtsbreite
Pos.: 14			2	33,0
Kunden Pos.: DG 03-03				Blindholz für PVC-Blindstock Universal
Stück: 1				

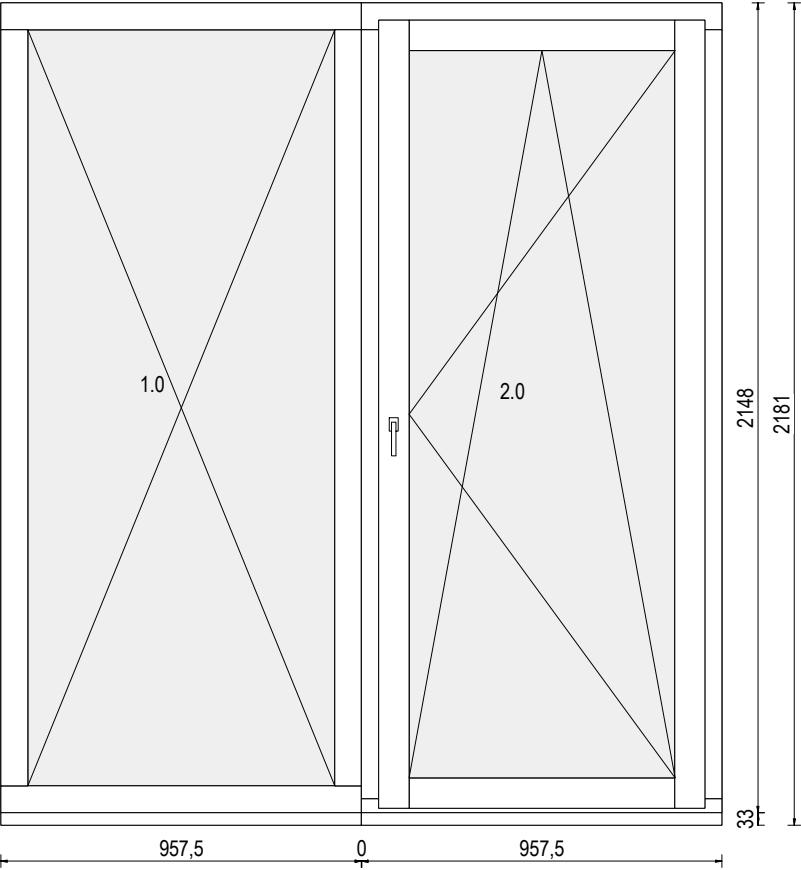

Elementübersicht

Seite: 13
Ried, am 15.07.2025
Druckzeit: 10:02:20

Auftragsnr.: 132475 HA

Techniker: sdo


Kommission: Moonlight - Söll, zu 132207 + 132476

Vertreter: rch

Kunde: Fenster, Türen, Parkett, Sonnenschutz SR.Schauraum GmbH

Fenstersystem: Rieder 98 HA Innen FB


Maßstab: 1:15
Pos.: 15
Kunden Pos.: DG 03-01
Stück: 1
Gesamt Außenmaß: 915,0 * 1205,0

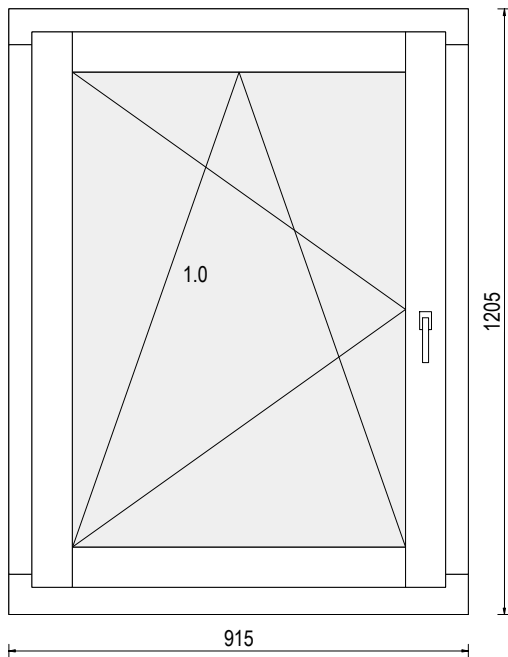

Elementübersicht

Auftragsnr.: 132475 HA			Techniker: sdo		
Kommission: Moonlight - Söll, zu 132207 + 132476			Vertreter: rch		
Kunde: Fenster, Türen, Parkett, Sonnenschutz SR.Schauraum GmbH					
Fenstersystem: Rieder 98 HA Innen FB					

Maßstab: 1:20	Gesamt Außenmaß: 1119,0 * 2188,0	Verbreiterungen:	Stück	Ansichtsbreite	
Pos.: 16			1	31,0	Rahmenverbreiterung 30-74 mm
Kunden Pos.: DG					
Stück: 1					

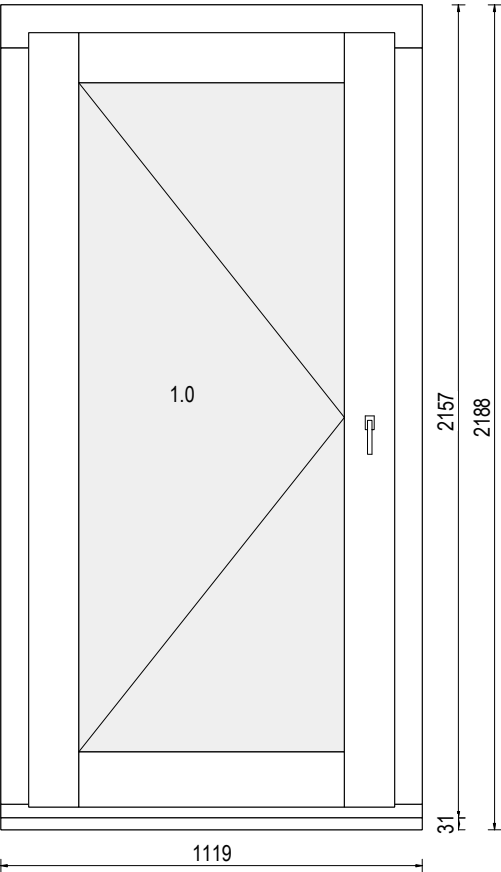

Elementübersicht

Seite: 15
Ried, am 15.07.2025
Druckzeit: 10:02:21

Auftragsnr.: 132475 HA

Techniker: sdo

Kommission: Moonlight - Söll, zu 132207 + 132476

Vertreter: rch

Kunde: Fenster, Türen, Parkett, Sonnenschutz SR.Schauraum GmbH

Fenstersystem: Rieder 98 HA Innen FB

Maßstab: 1:15
Pos.: 17
Kunden Pos.: DG
Stück: 1
Gesamt Außenmaß: 1220,0 * 1216,0

